



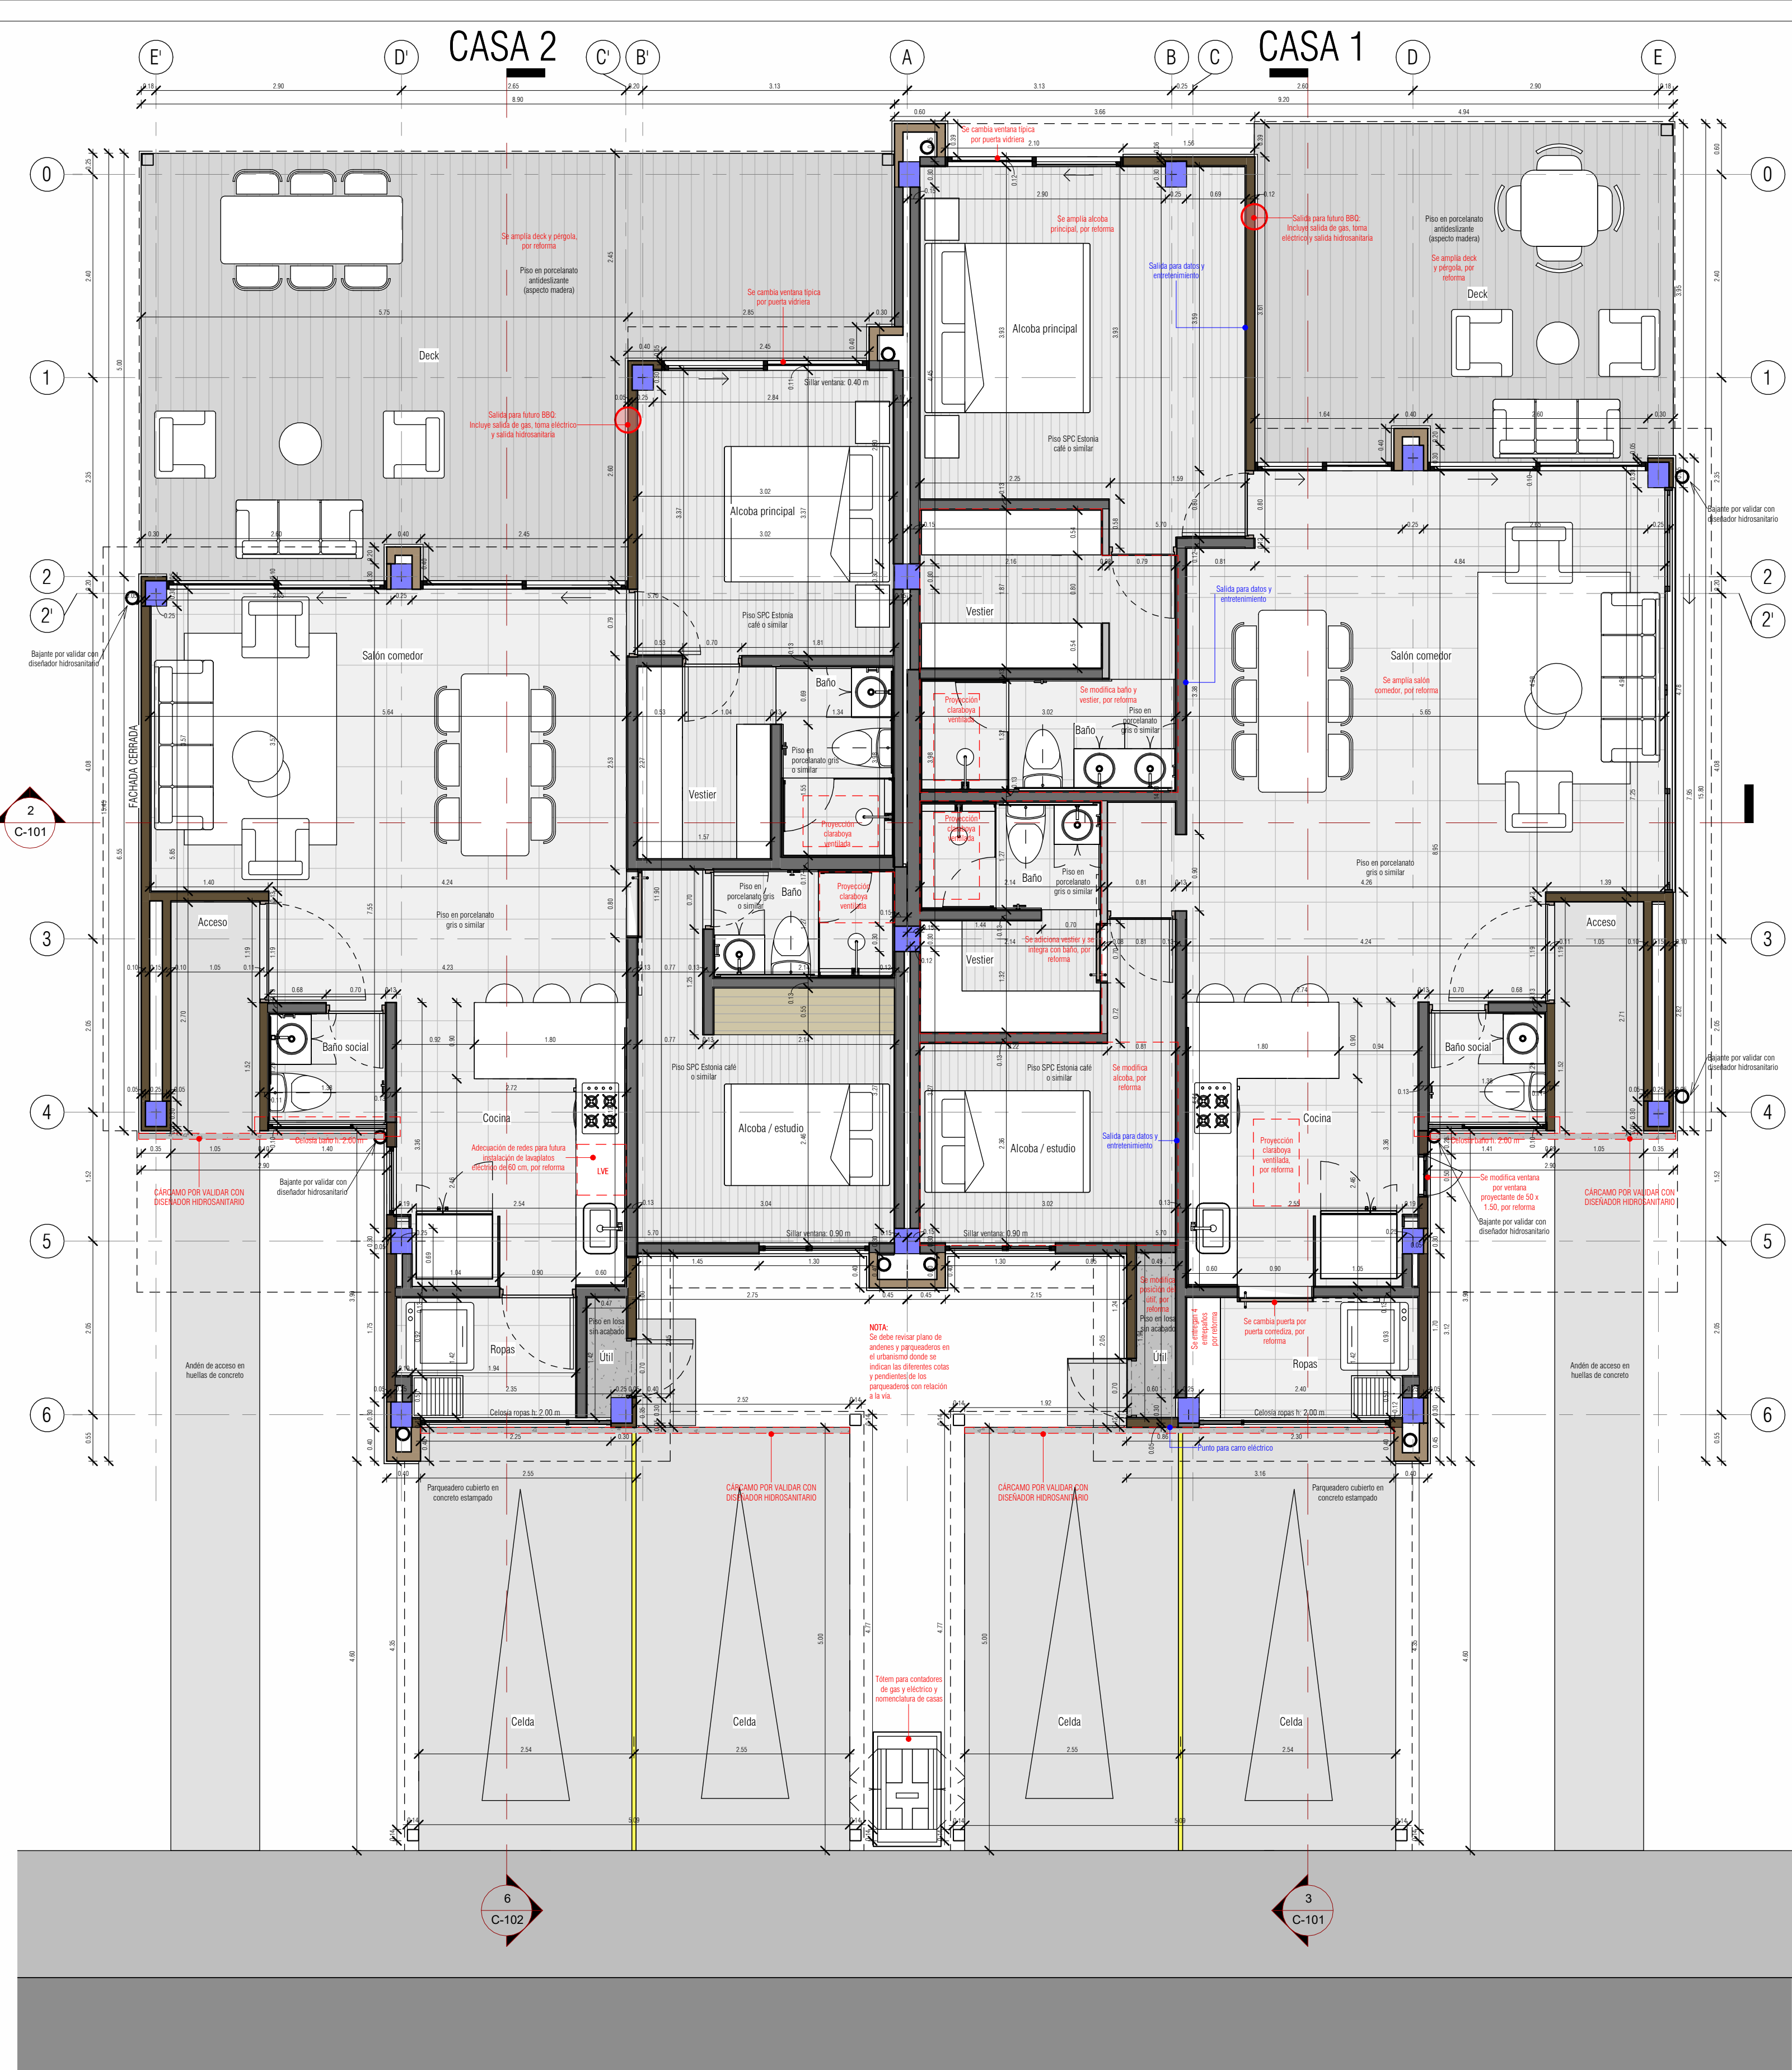

1 PLANTA - CASAS 1 Y 2
1:50

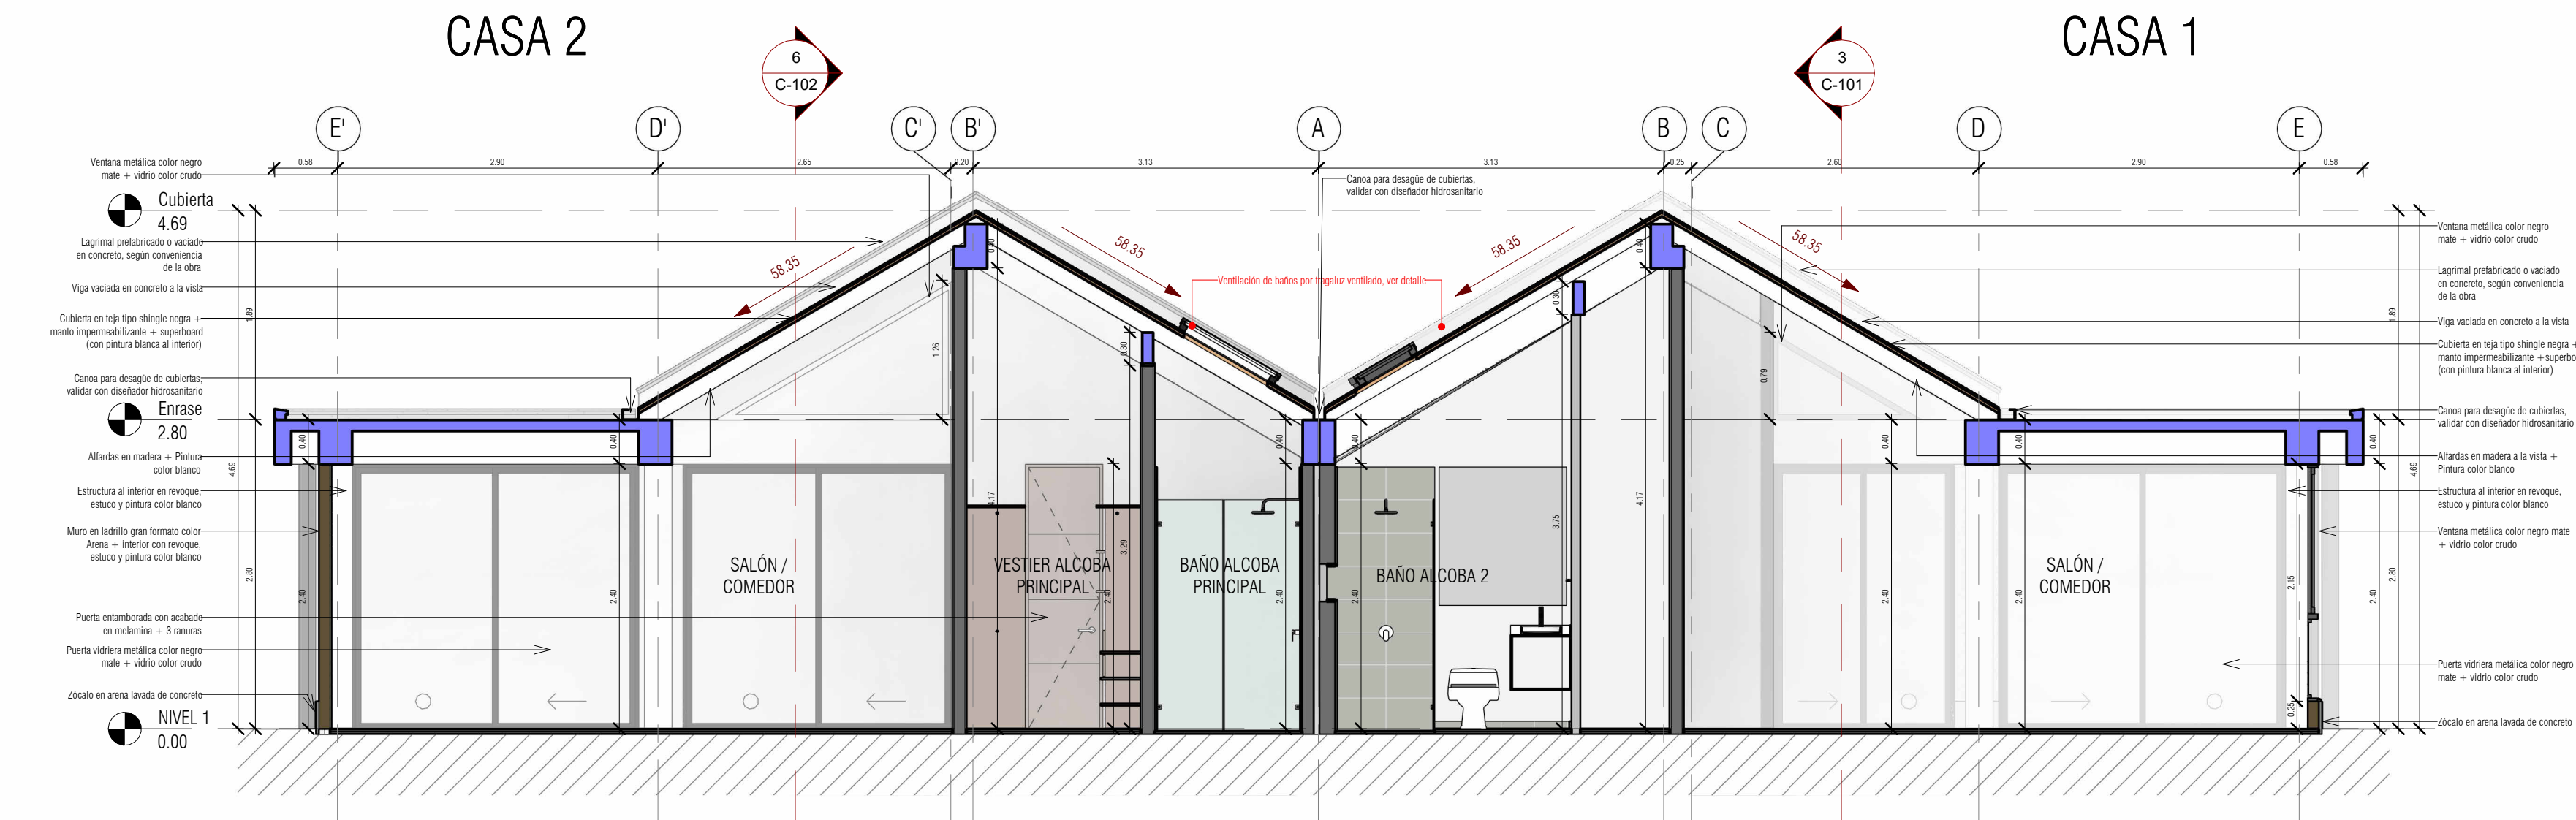

2 SECCIÓN TRANSVERSAL - CASAS 1 Y 2
1:50

REFORMAS:

CASA 1:

- Se amplía ropas y se adiciona mueble con 4 entrepaños.
- Se mueve y amplía útil.
- Se adiciona claraboya en cocina.
- Se modifica ventana de cocina por ventana proyectante de 0.50 x 1.50.
- Se reduce alcoba 2.
- Se adiciona vestier a alcoba 2 y se integra con baño.
- Se amplía alcoba principal.
- Se modifica baño y vestier de alcoba principal.
- Se amplía salón comedor.
- Se cambia ventana de alcoba principal por puerta vidriera de 2.10.
- Se amplía deck y pérgola.
- Se adicionan salidas de gas, eléctricas e hidrosanitarias para futuro BBQ.

REFORMAS ELÉCTRICAS

- Punto para carro eléctrico.
- Punto para datos y entretenimiento en alcobas y salón comedor.


ÁREA CONSTRUIDA
CASA 1
ÁREA LICENCIADA: 137,99 m²
ÁREA REFORMA: 24,40 m²
ÁREA TOTAL: 162,39 m²

ÁREA PRIVADA
CASA 1
154,99m²

ÁREA CONSTRUIDA
CASA 2
ÁREA LICENCIADA: 137,99 m²
ÁREA REFORMA: 19,42 m²
ÁREA TOTAL: 157,41 m²

ÁREA PRIVADA
CASA 2
150,84 m²


VÁLIDO PARA
CASAS 1 Y 2

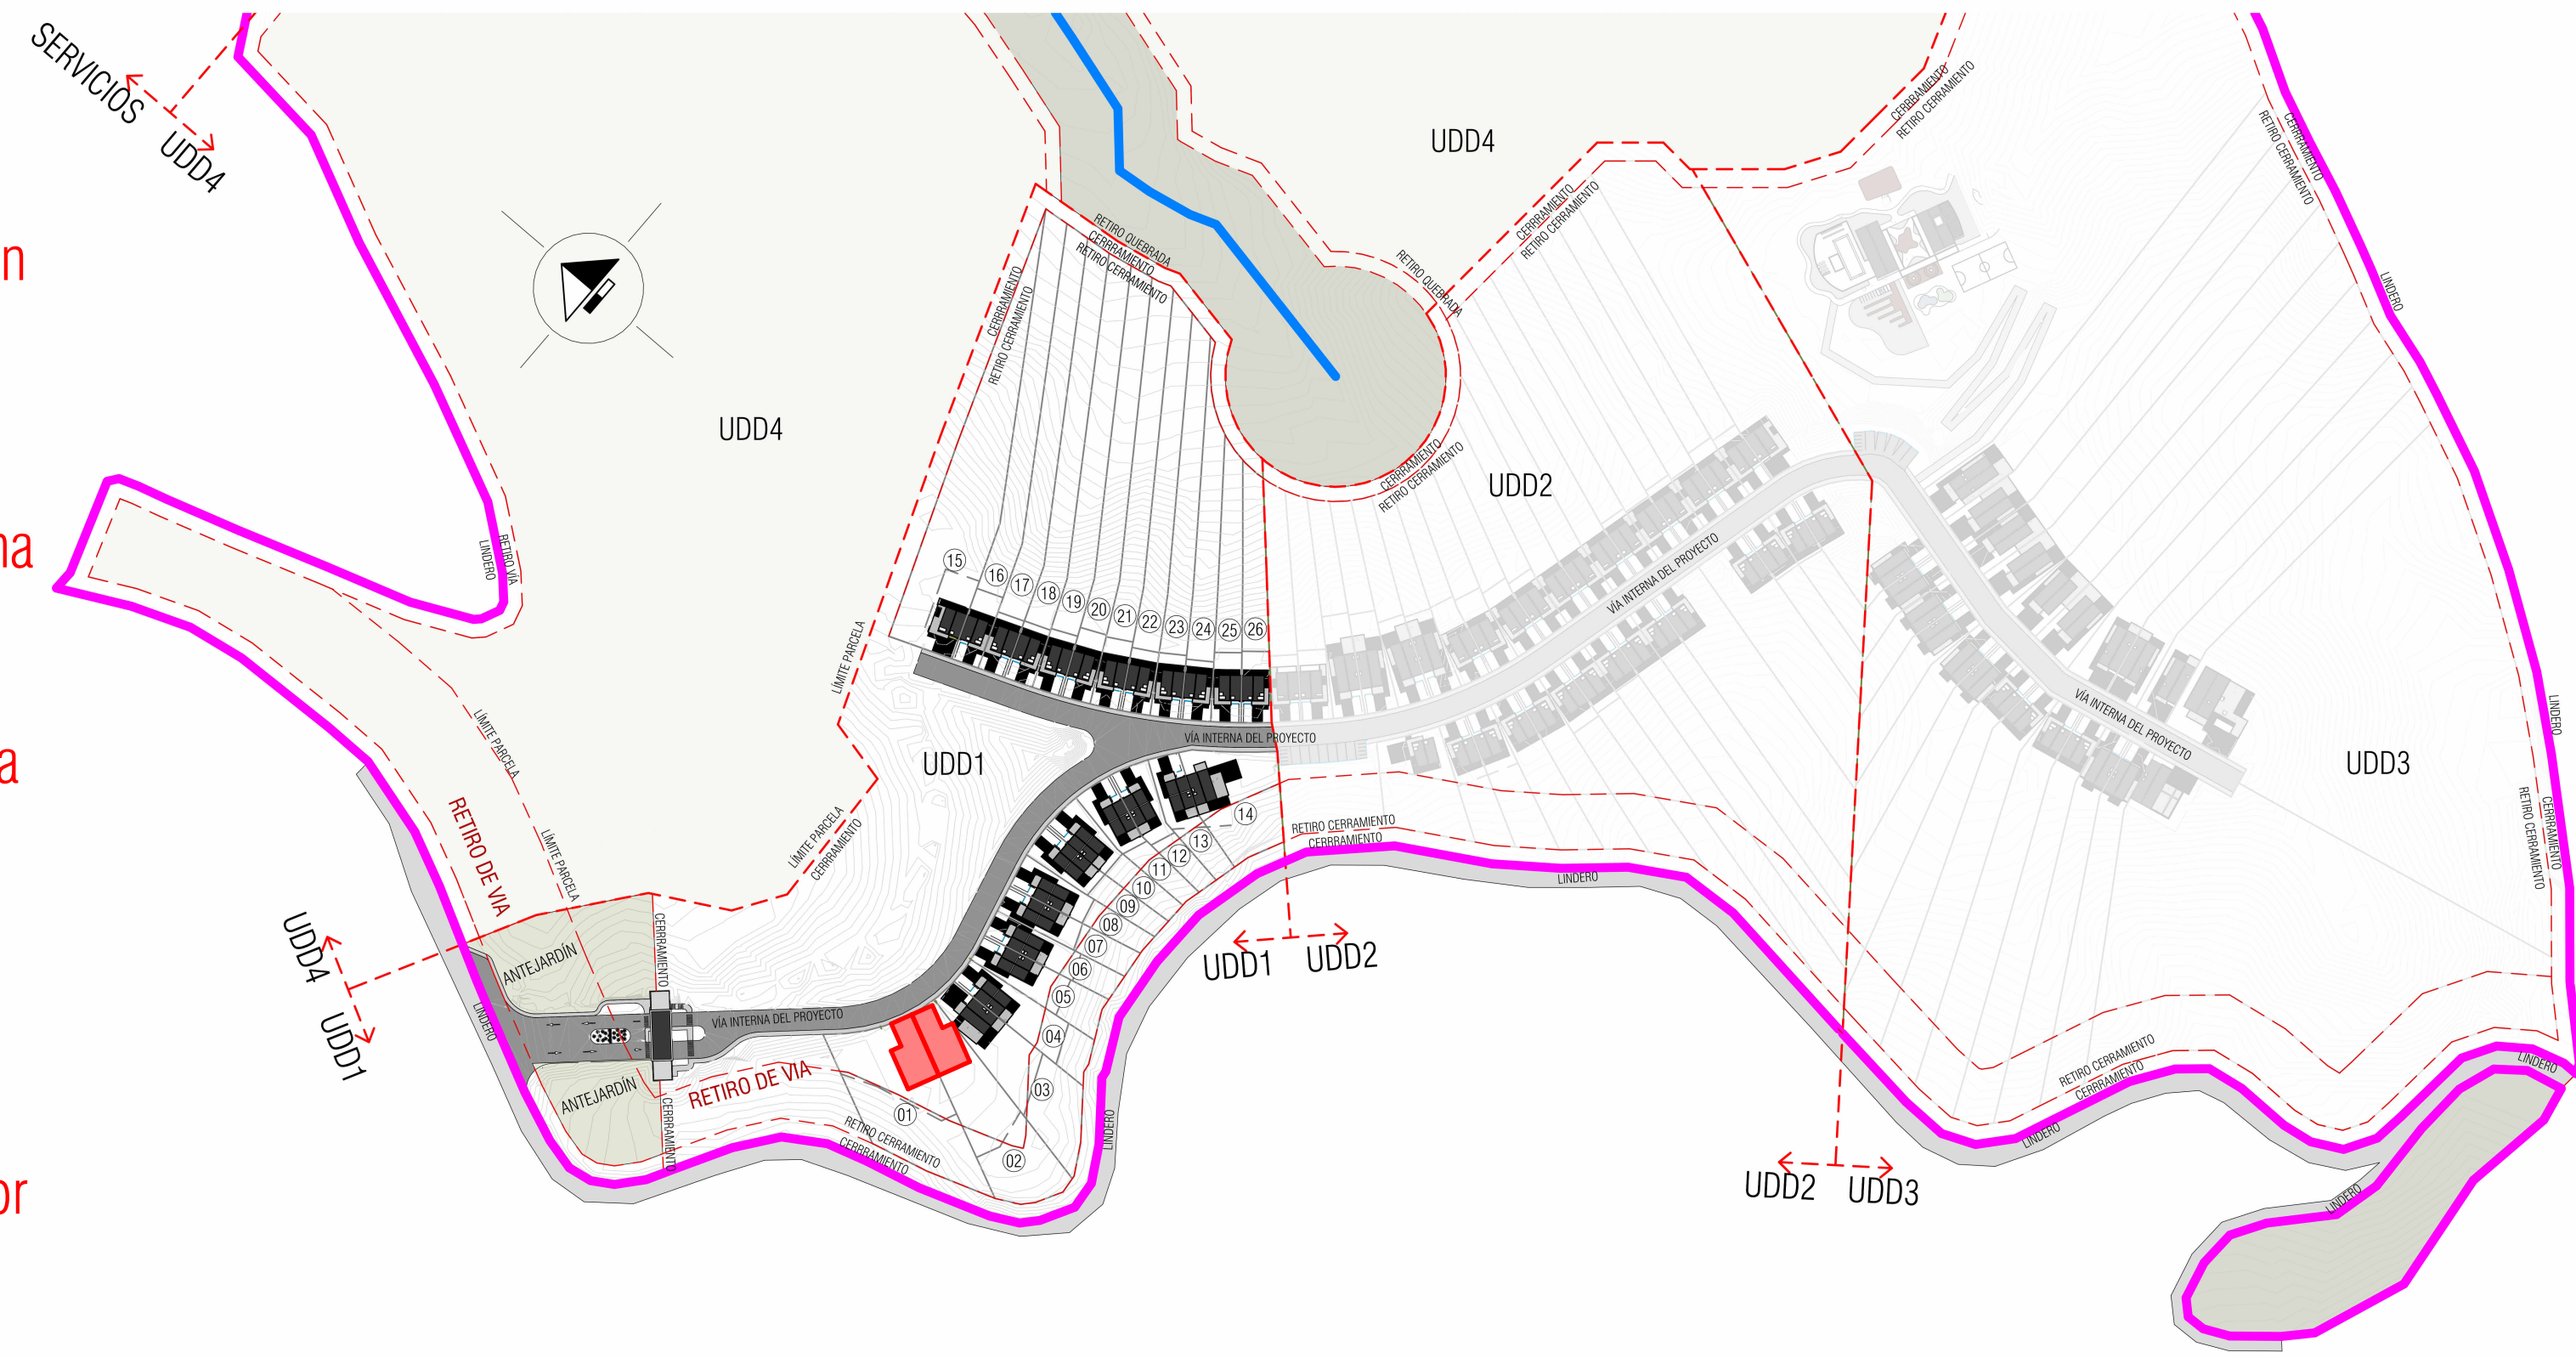


LOCALIZACIÓN CASAS 1 Y 2
1:1

CASA 2:

- Se adicionan salidas para futuro Lavaplatos eléctrico en cocina.
- Se cambia ventana de alcoba principal por puerta vidriera de 2.10.
- Se amplía deck y pérgola.
- Se adicionan salidas de gas, eléctricas e hidrosanitarias para futuro BBQ.

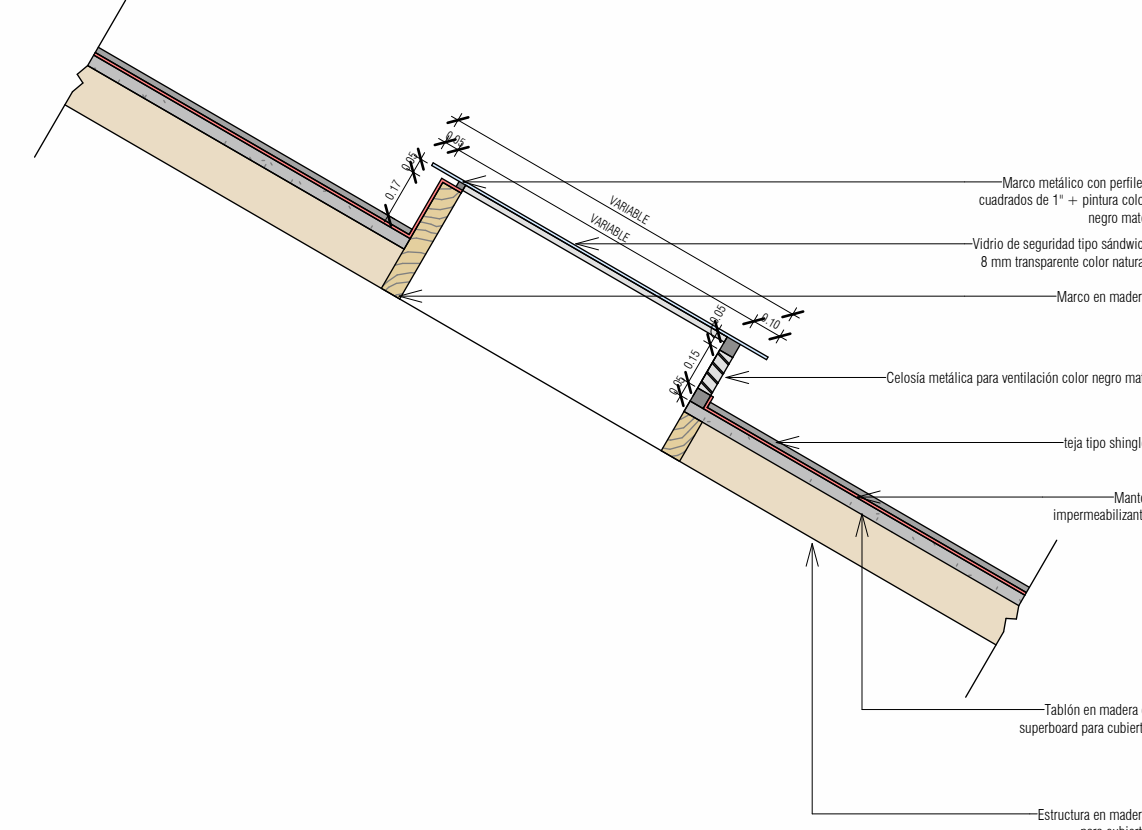

DETALLE CLARABOYA VENTILADA PARA BAÑOS
1:25

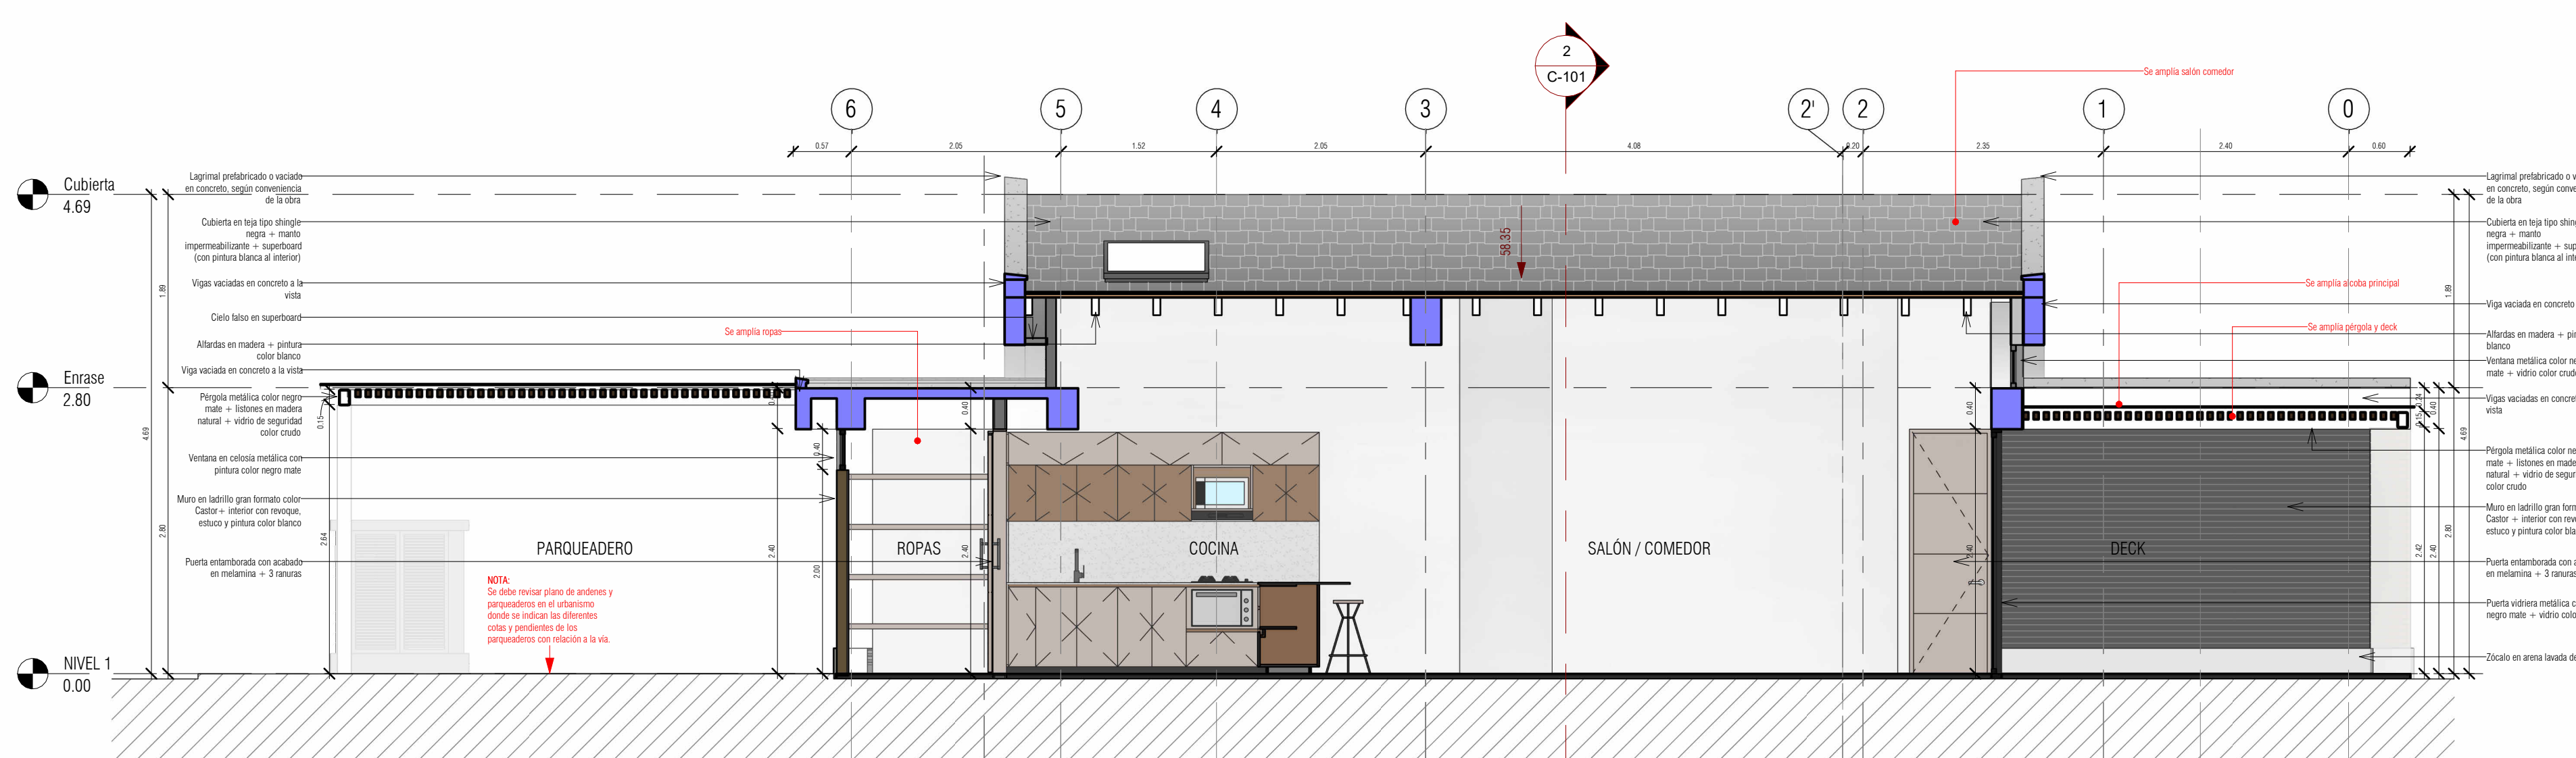

3 SECCIÓN LONGITUDINAL - CASA 1
1:50