



PLANTA PERGOLA EN DECK

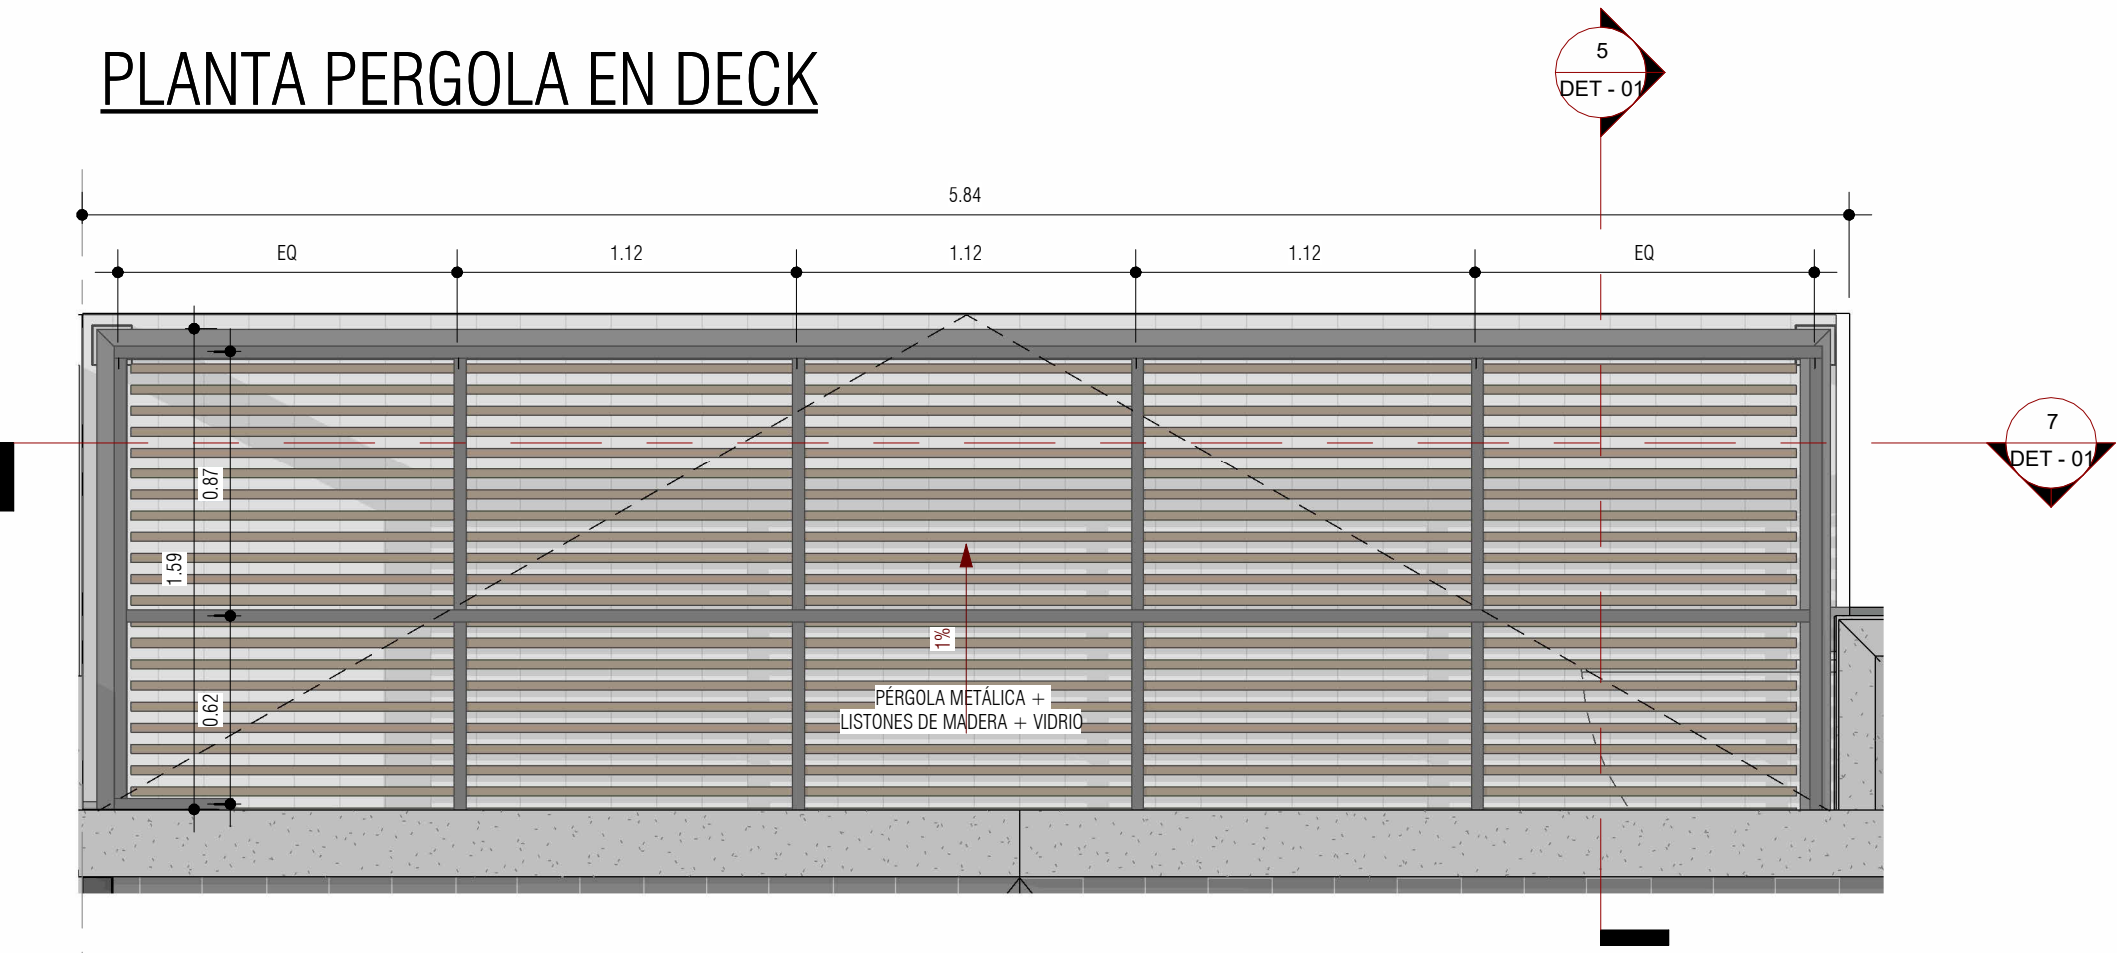


2 PERGOLA DECK - CASA 16
1:25


PLANTA PERGOLA EN PARQUEADERO + ACCESO PEATONAL

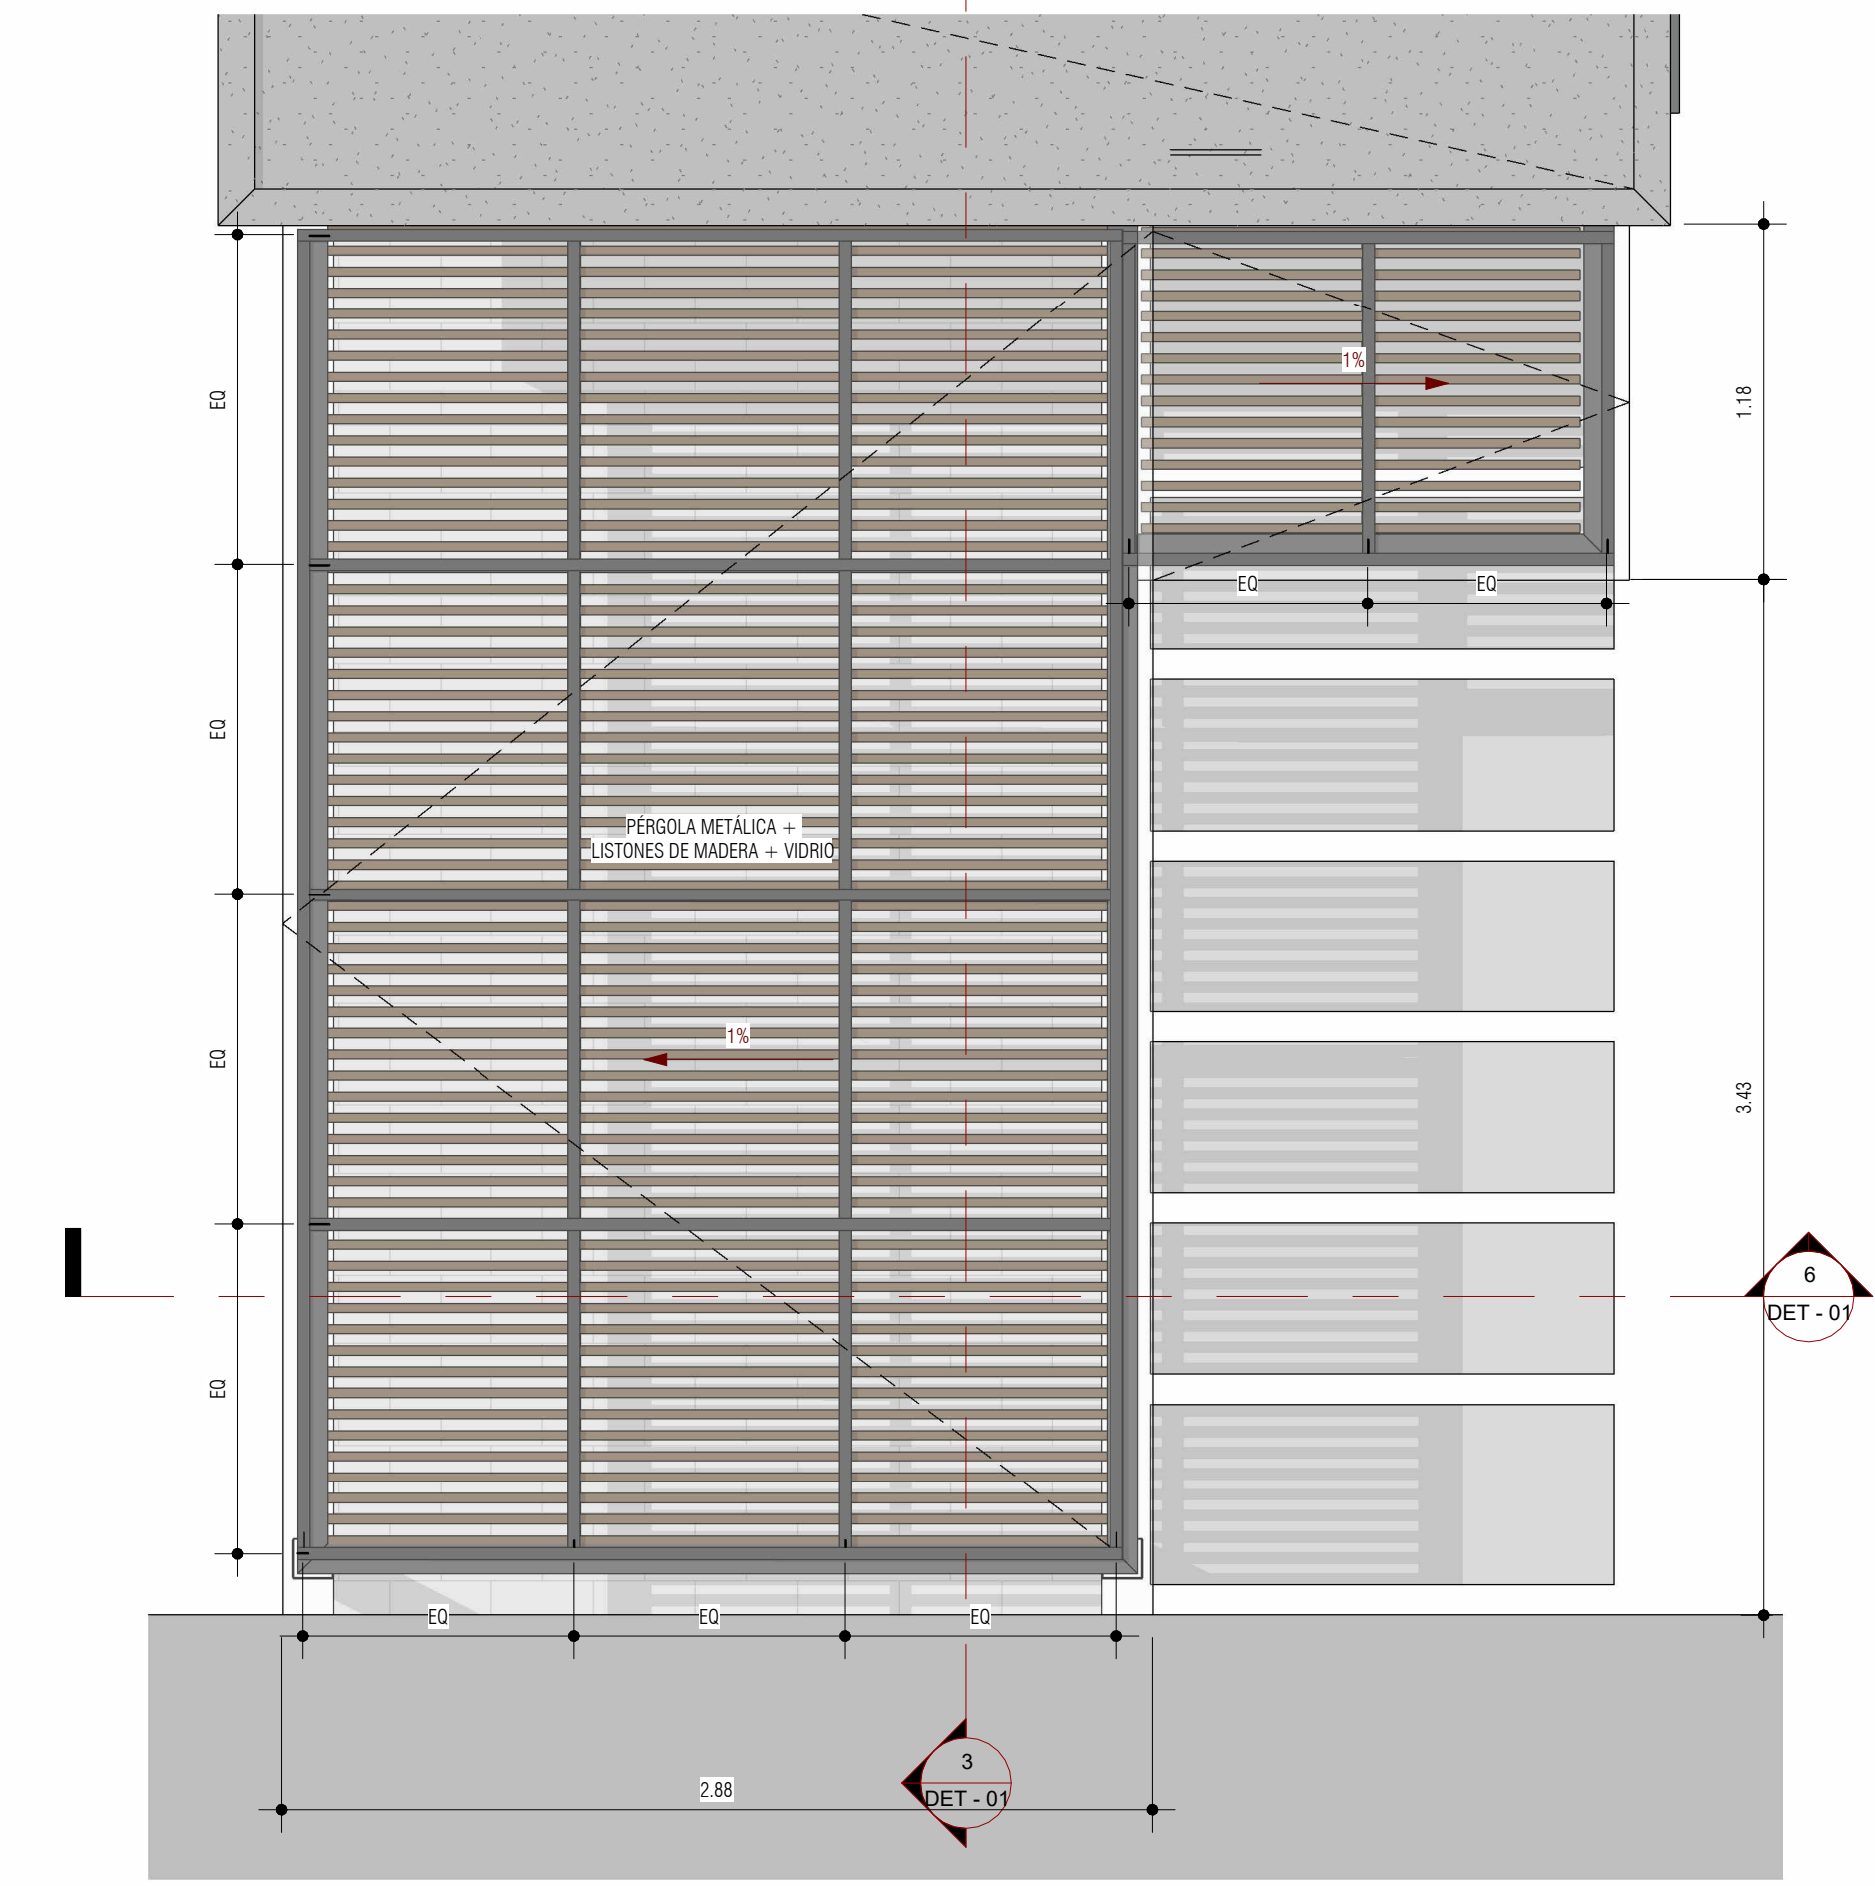

4 PERGOLA PARQUEADERO - CASA 16
1:25

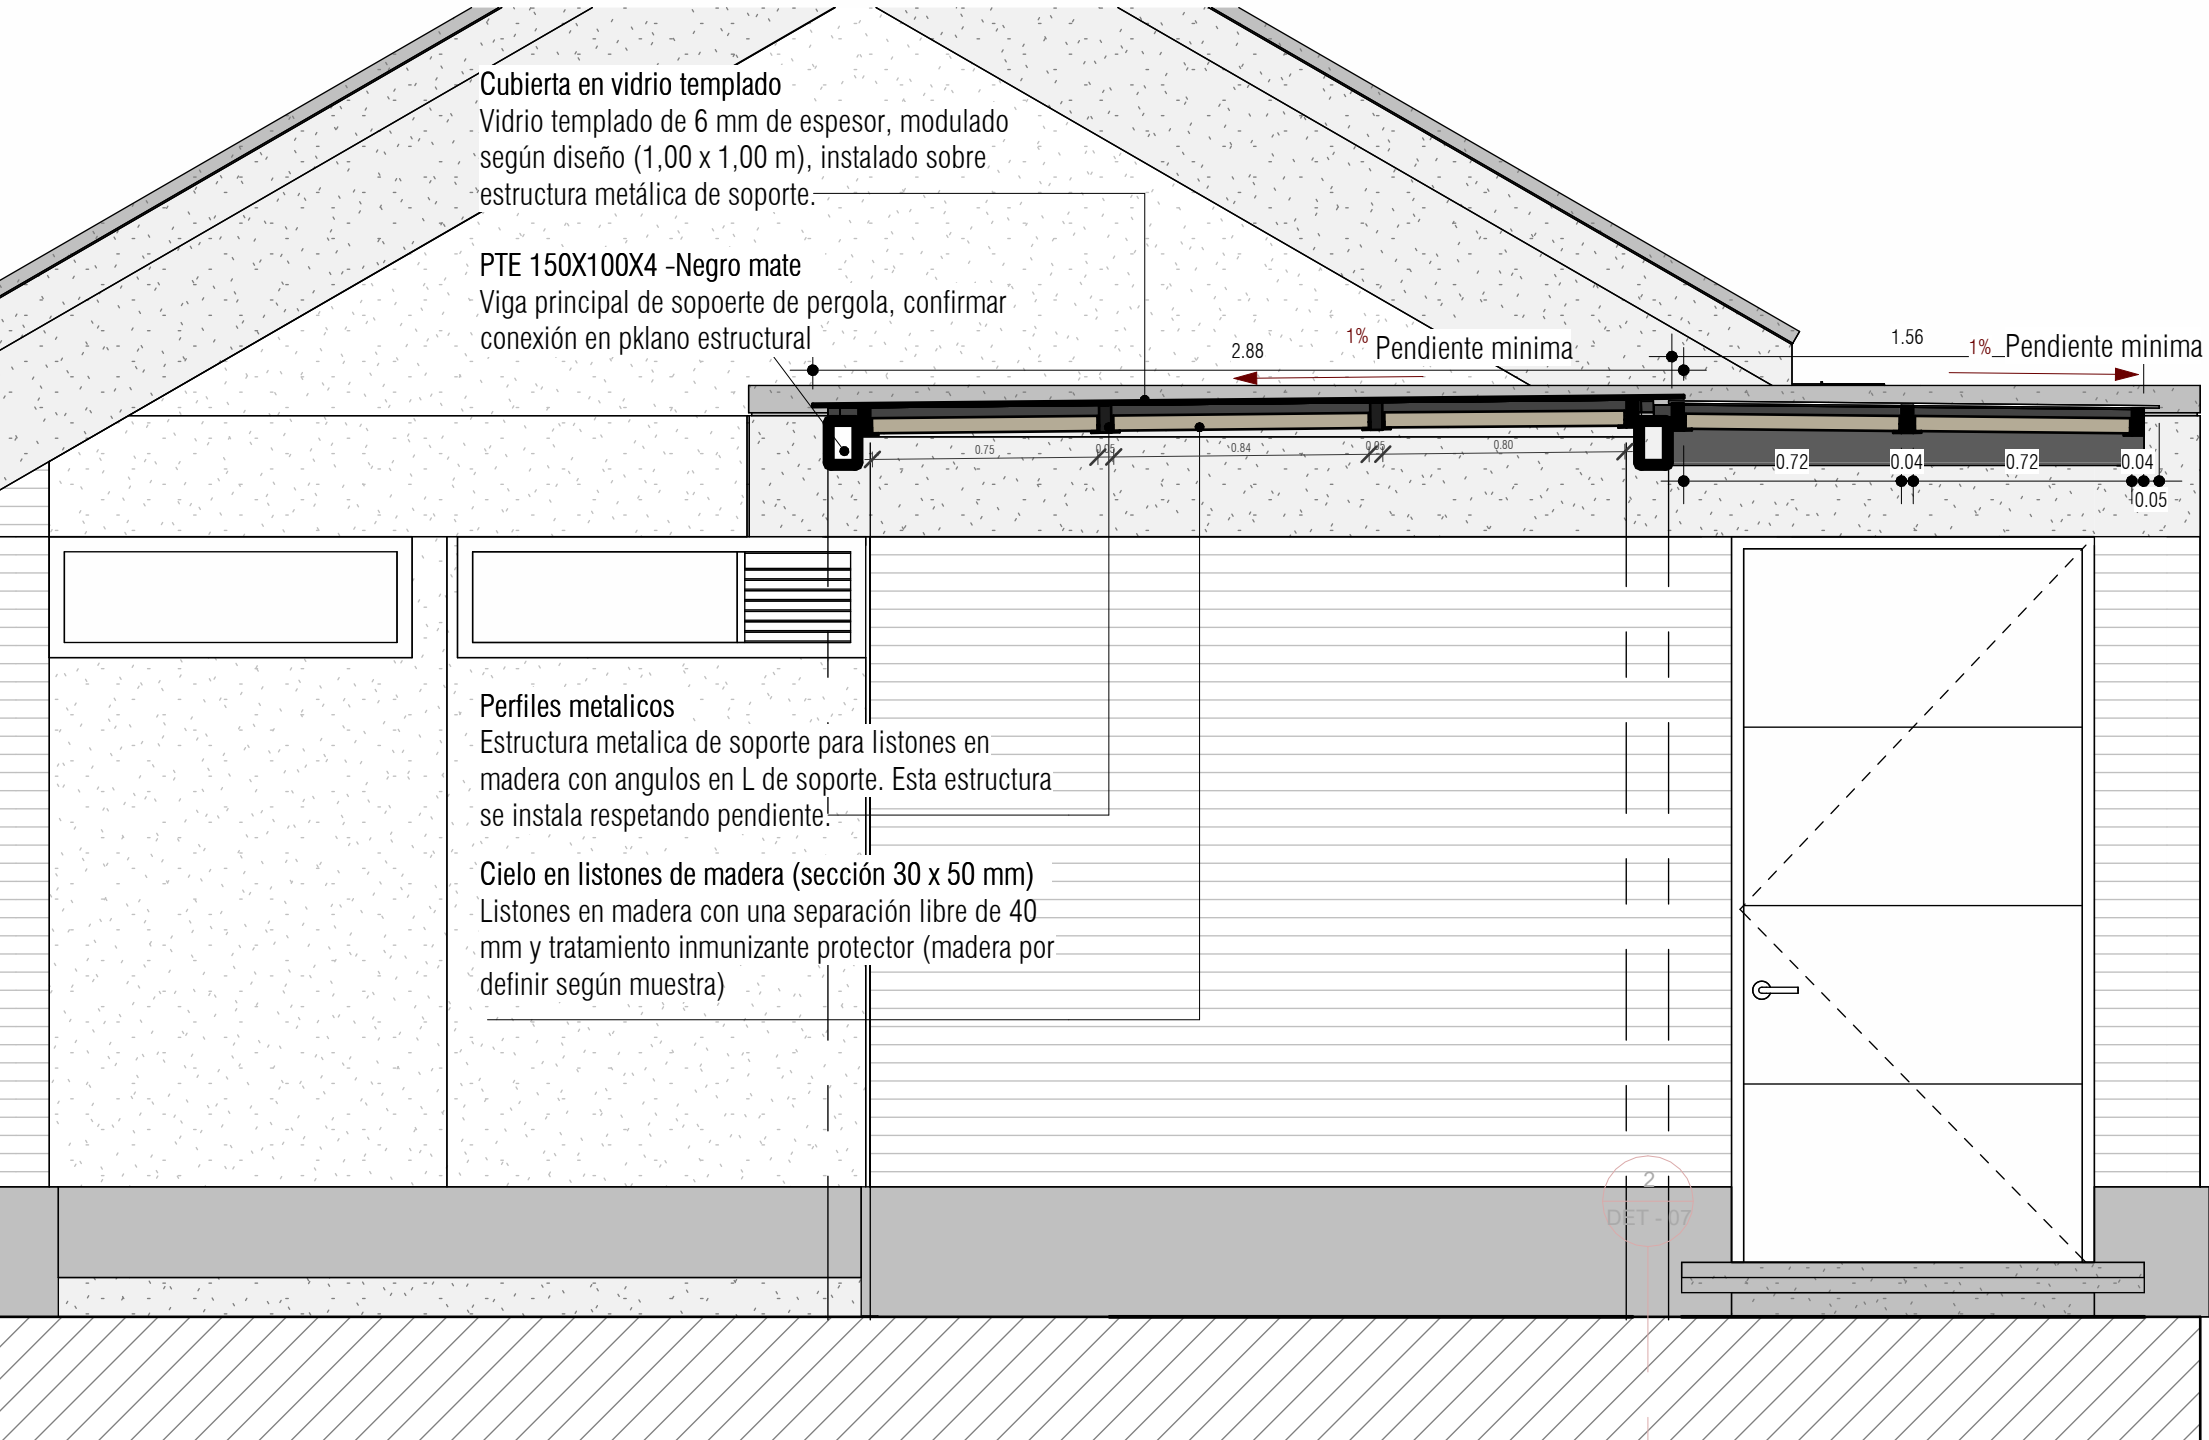


6 CORTE POR FACHDA TRANS - PERGOLA PARQUEADERO
1:25

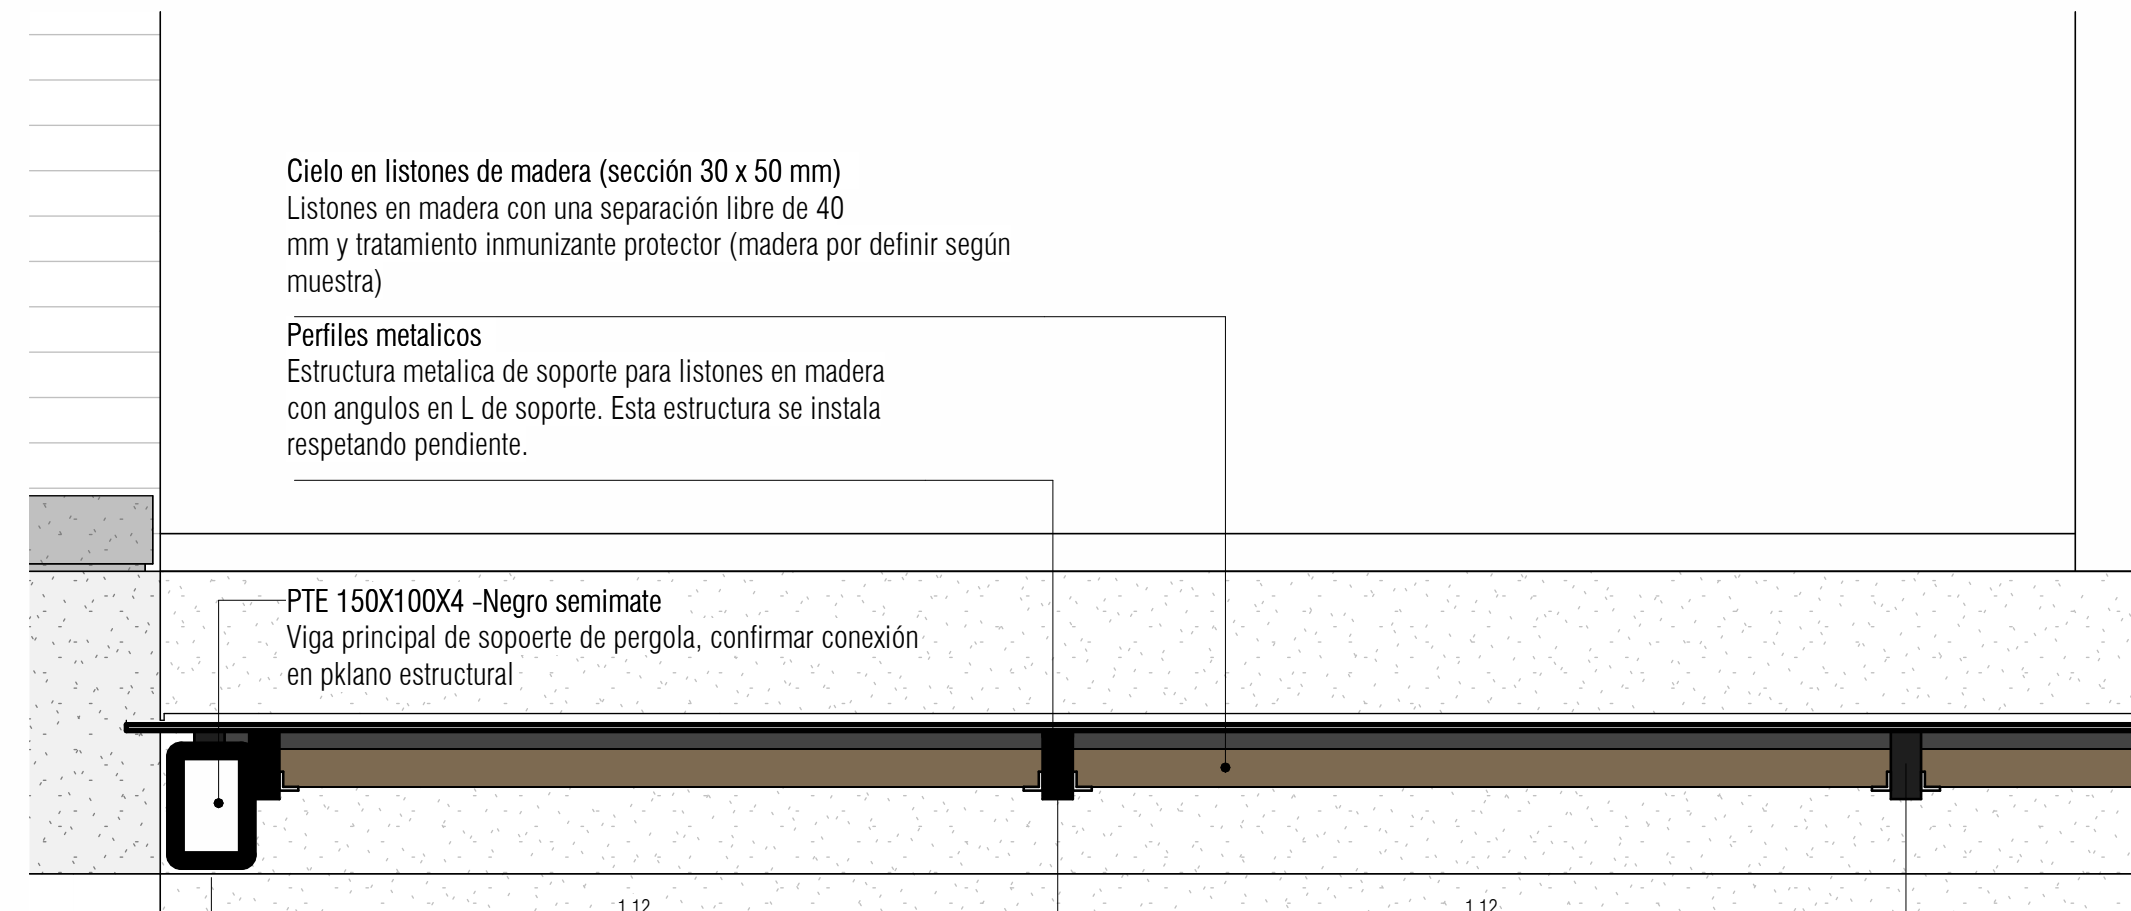


7 CORTE FACHADA PERGOLA DECK - DET-01
1:10

DETALLE ANCLAJE A VIGA DE ENRASE

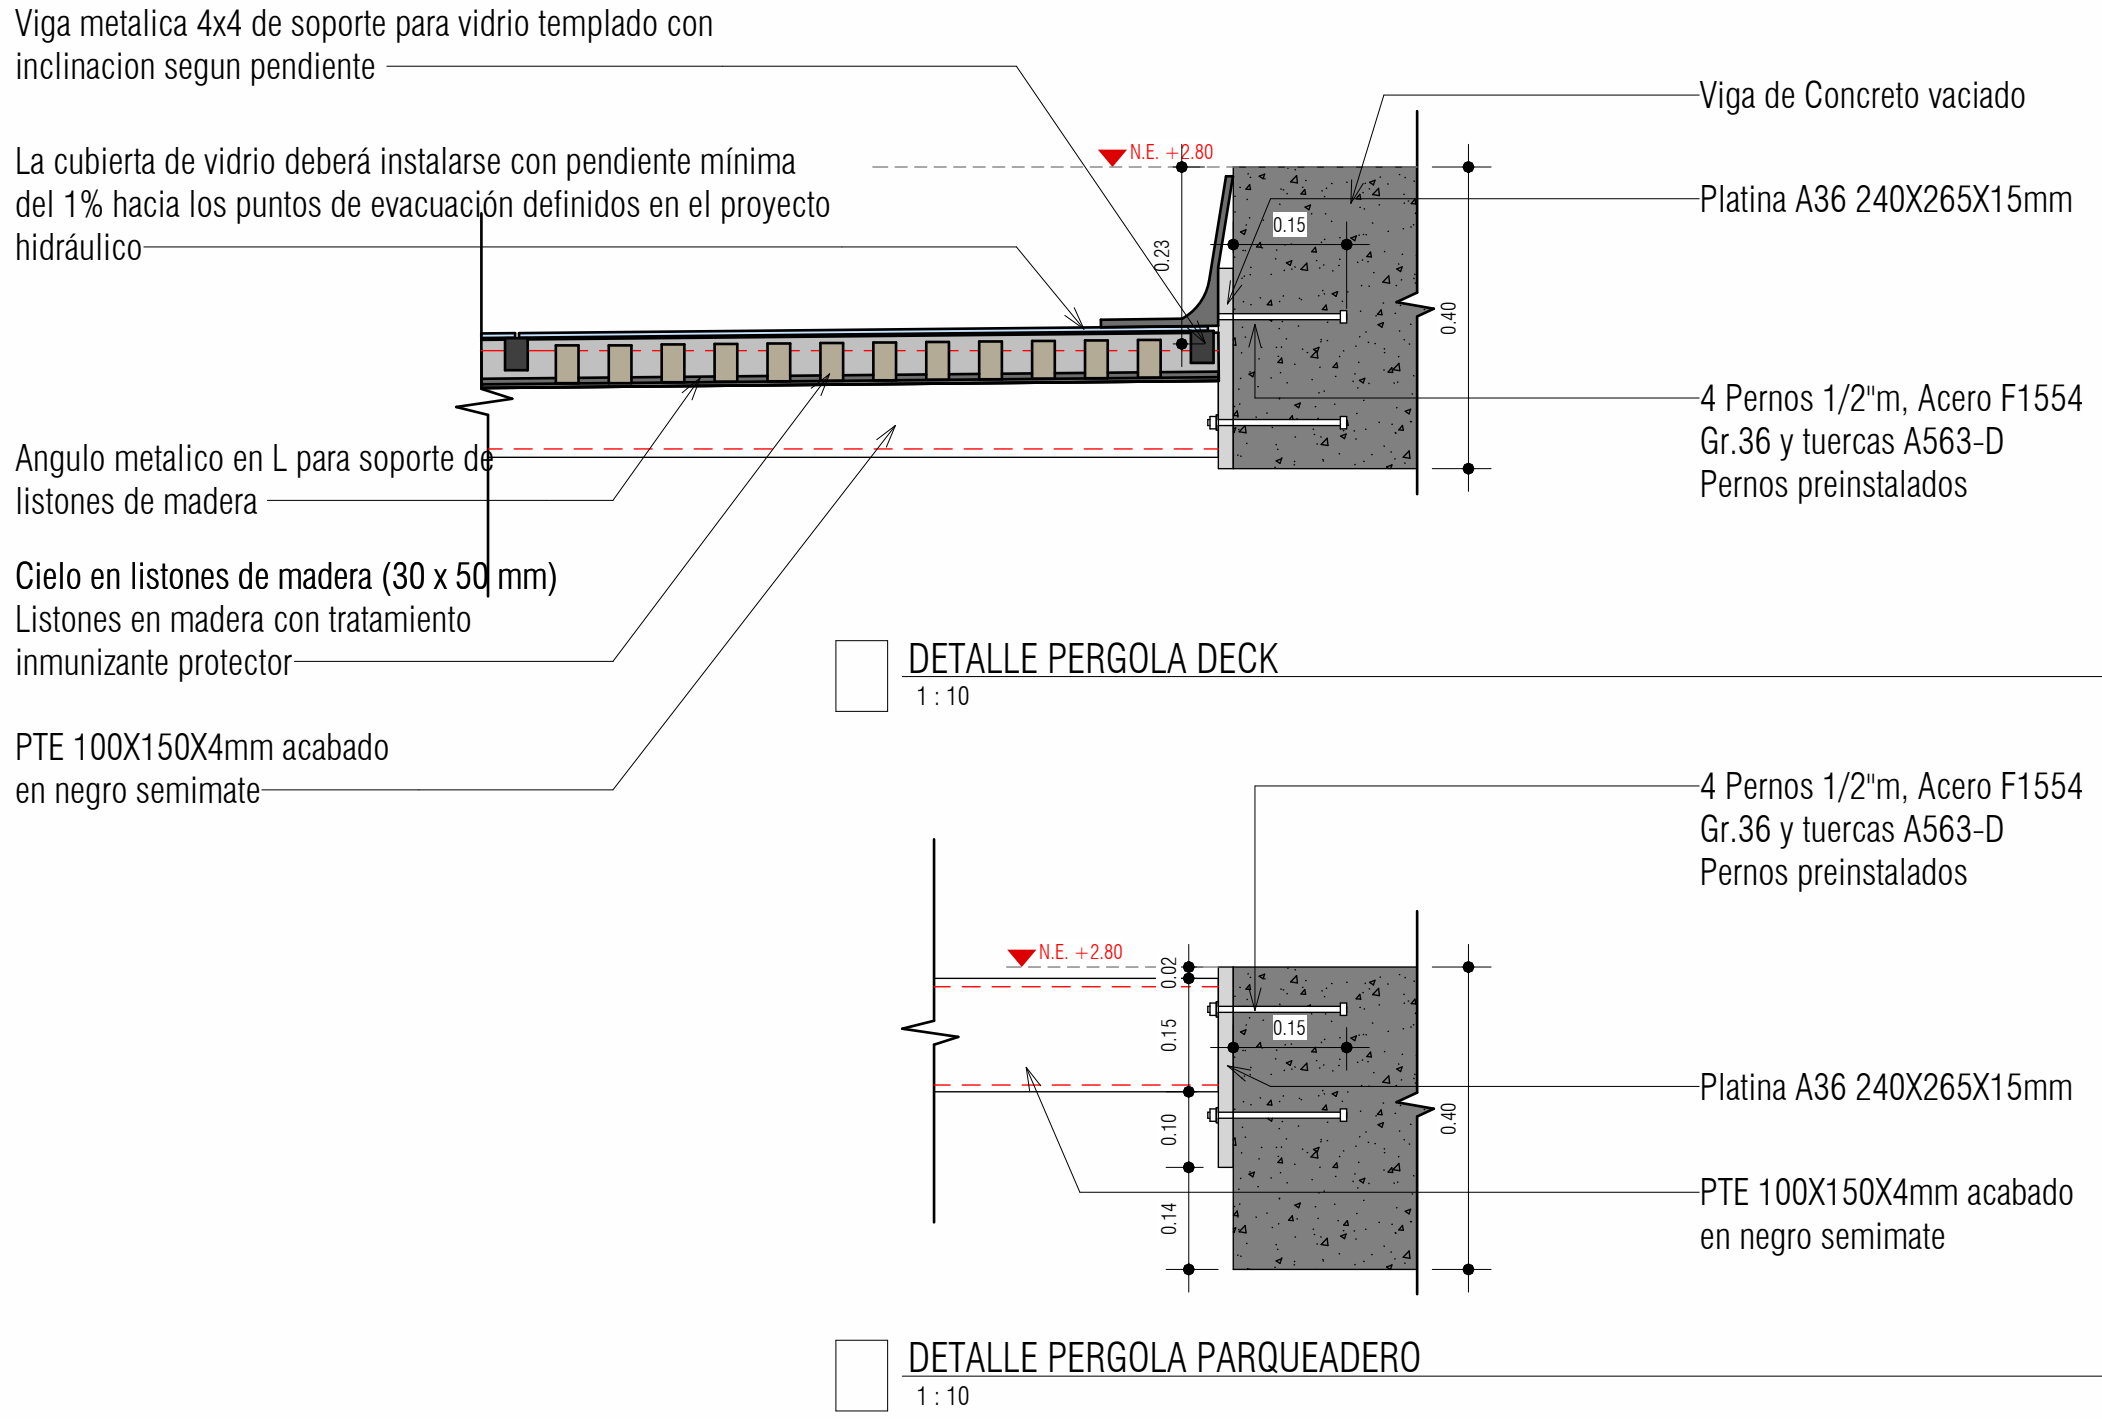


DETALLE PERGOLA PARQUEADERO
1:10

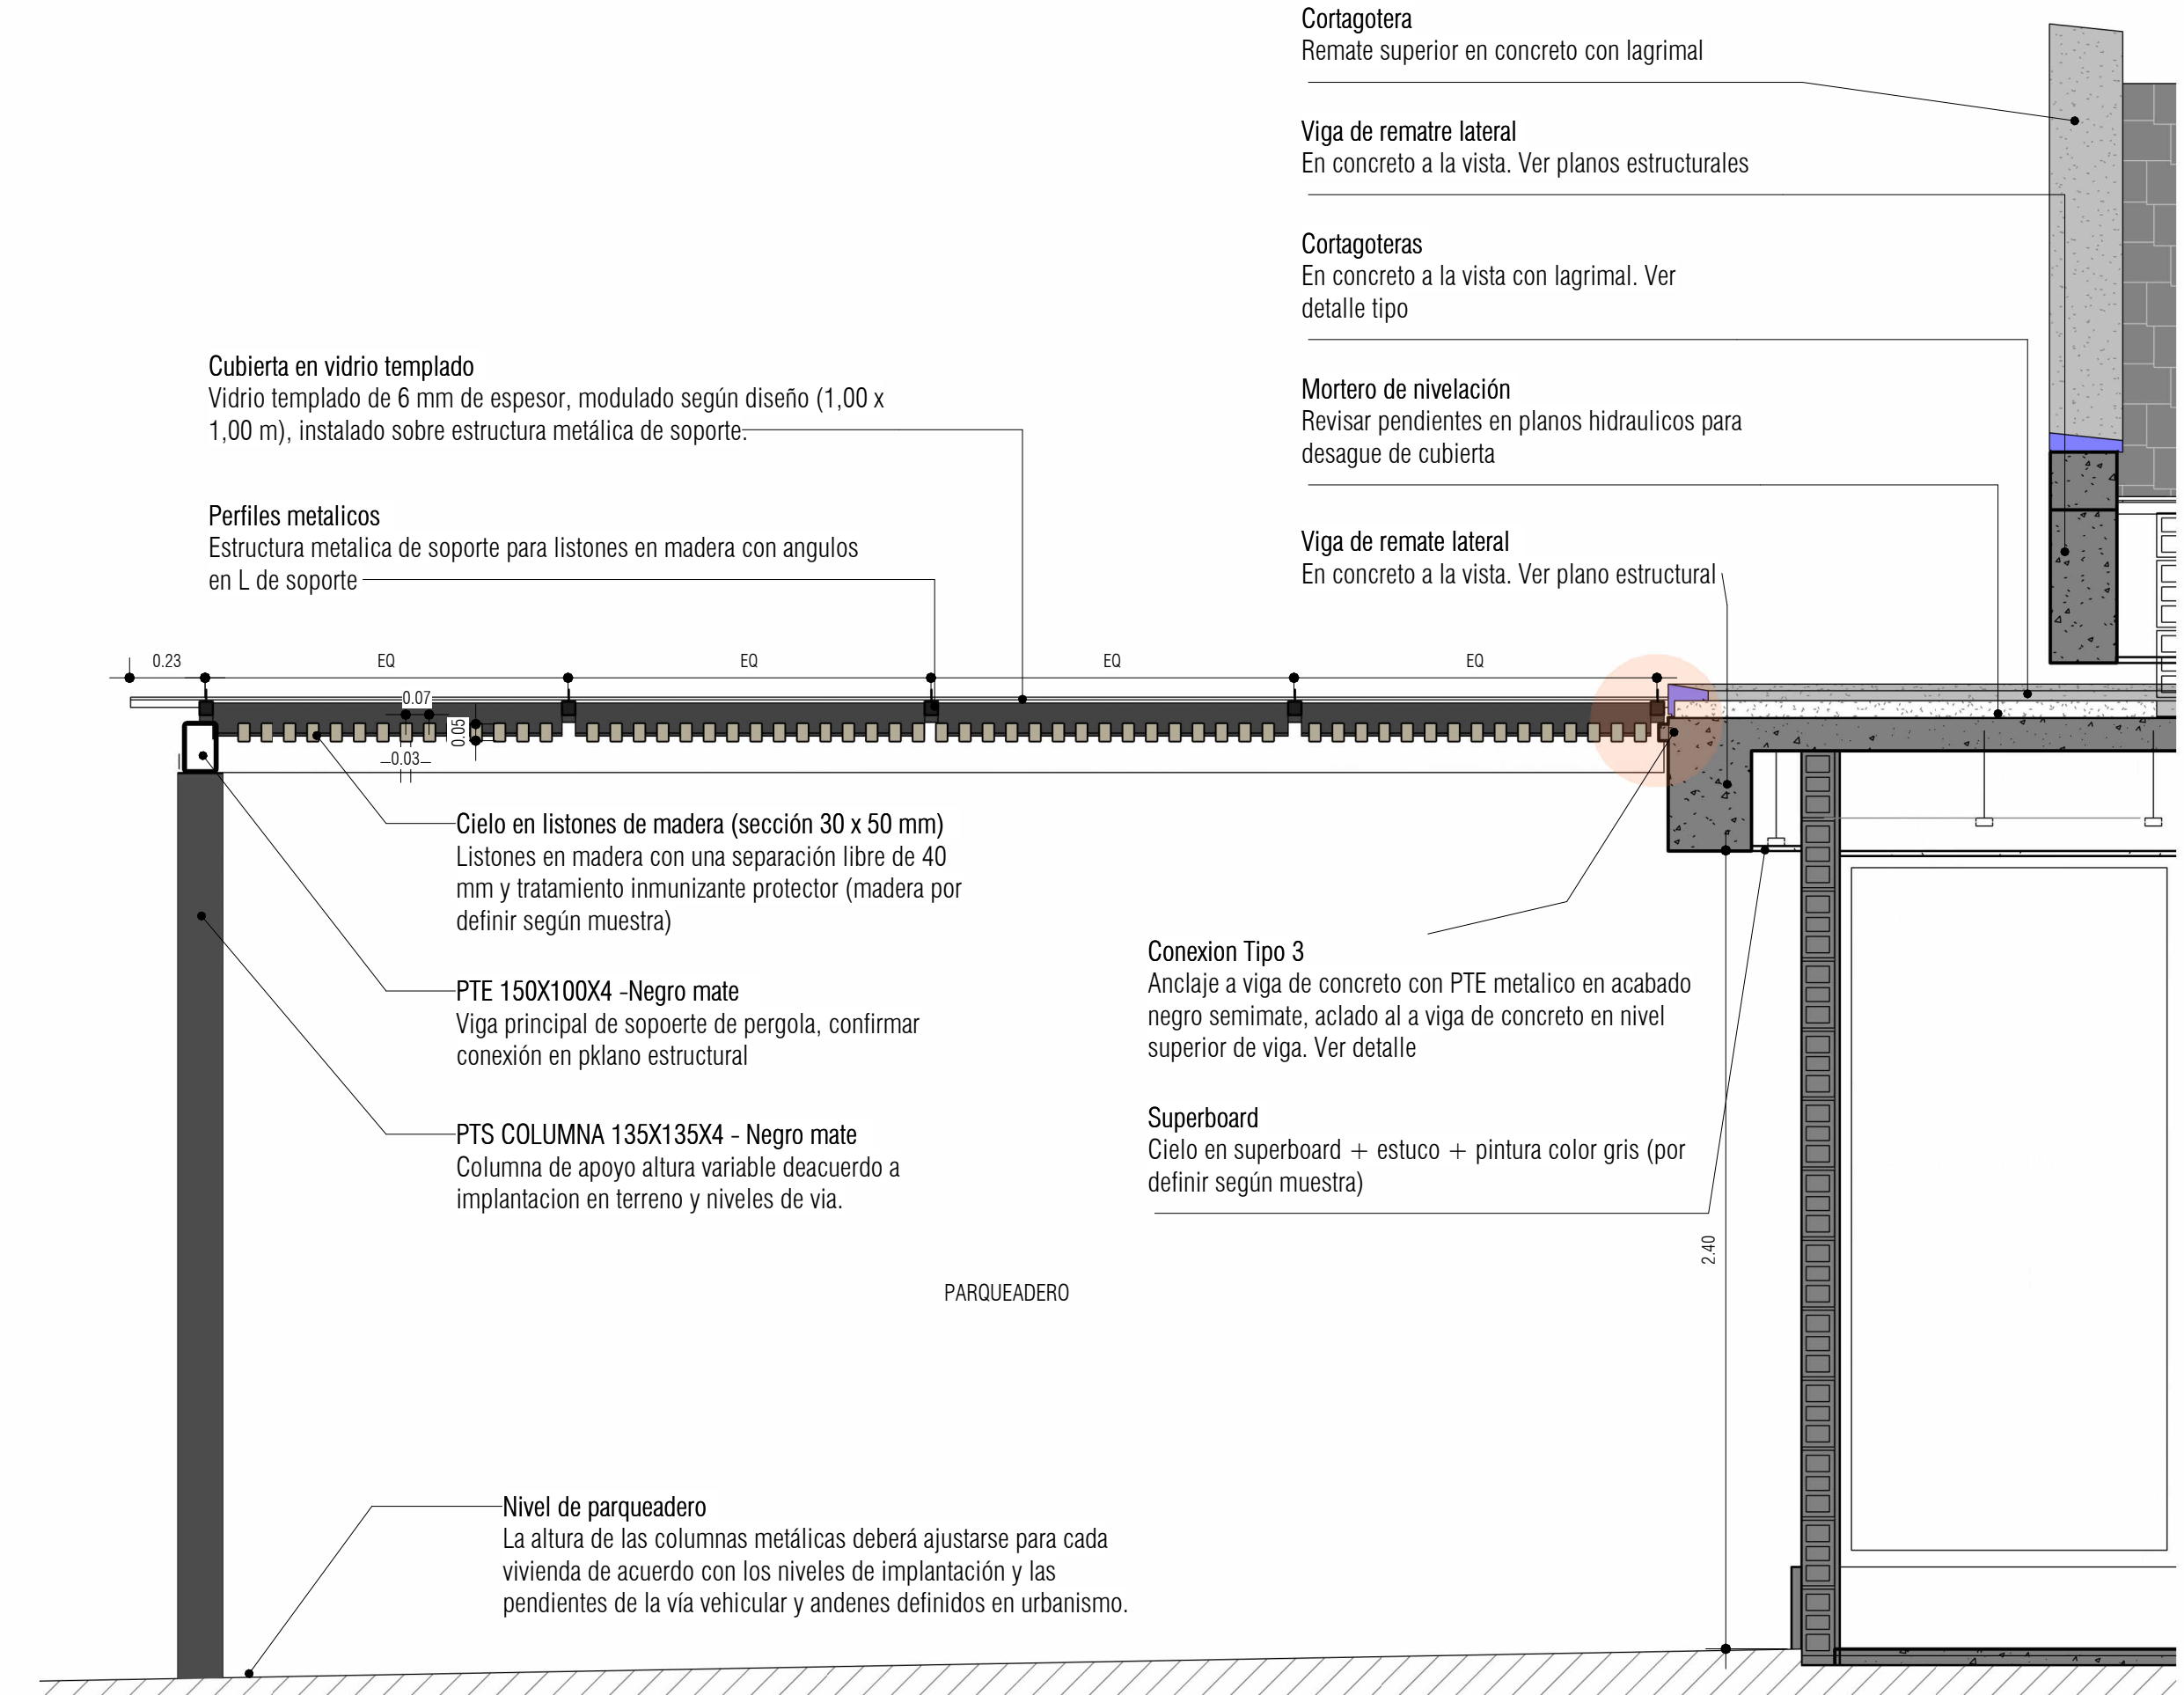

3 CORTE POR FACHADA LONG - PERGOLA - CASA 16
1:20

DETALLE PERGOLA
REFERENCIA CASAS 16

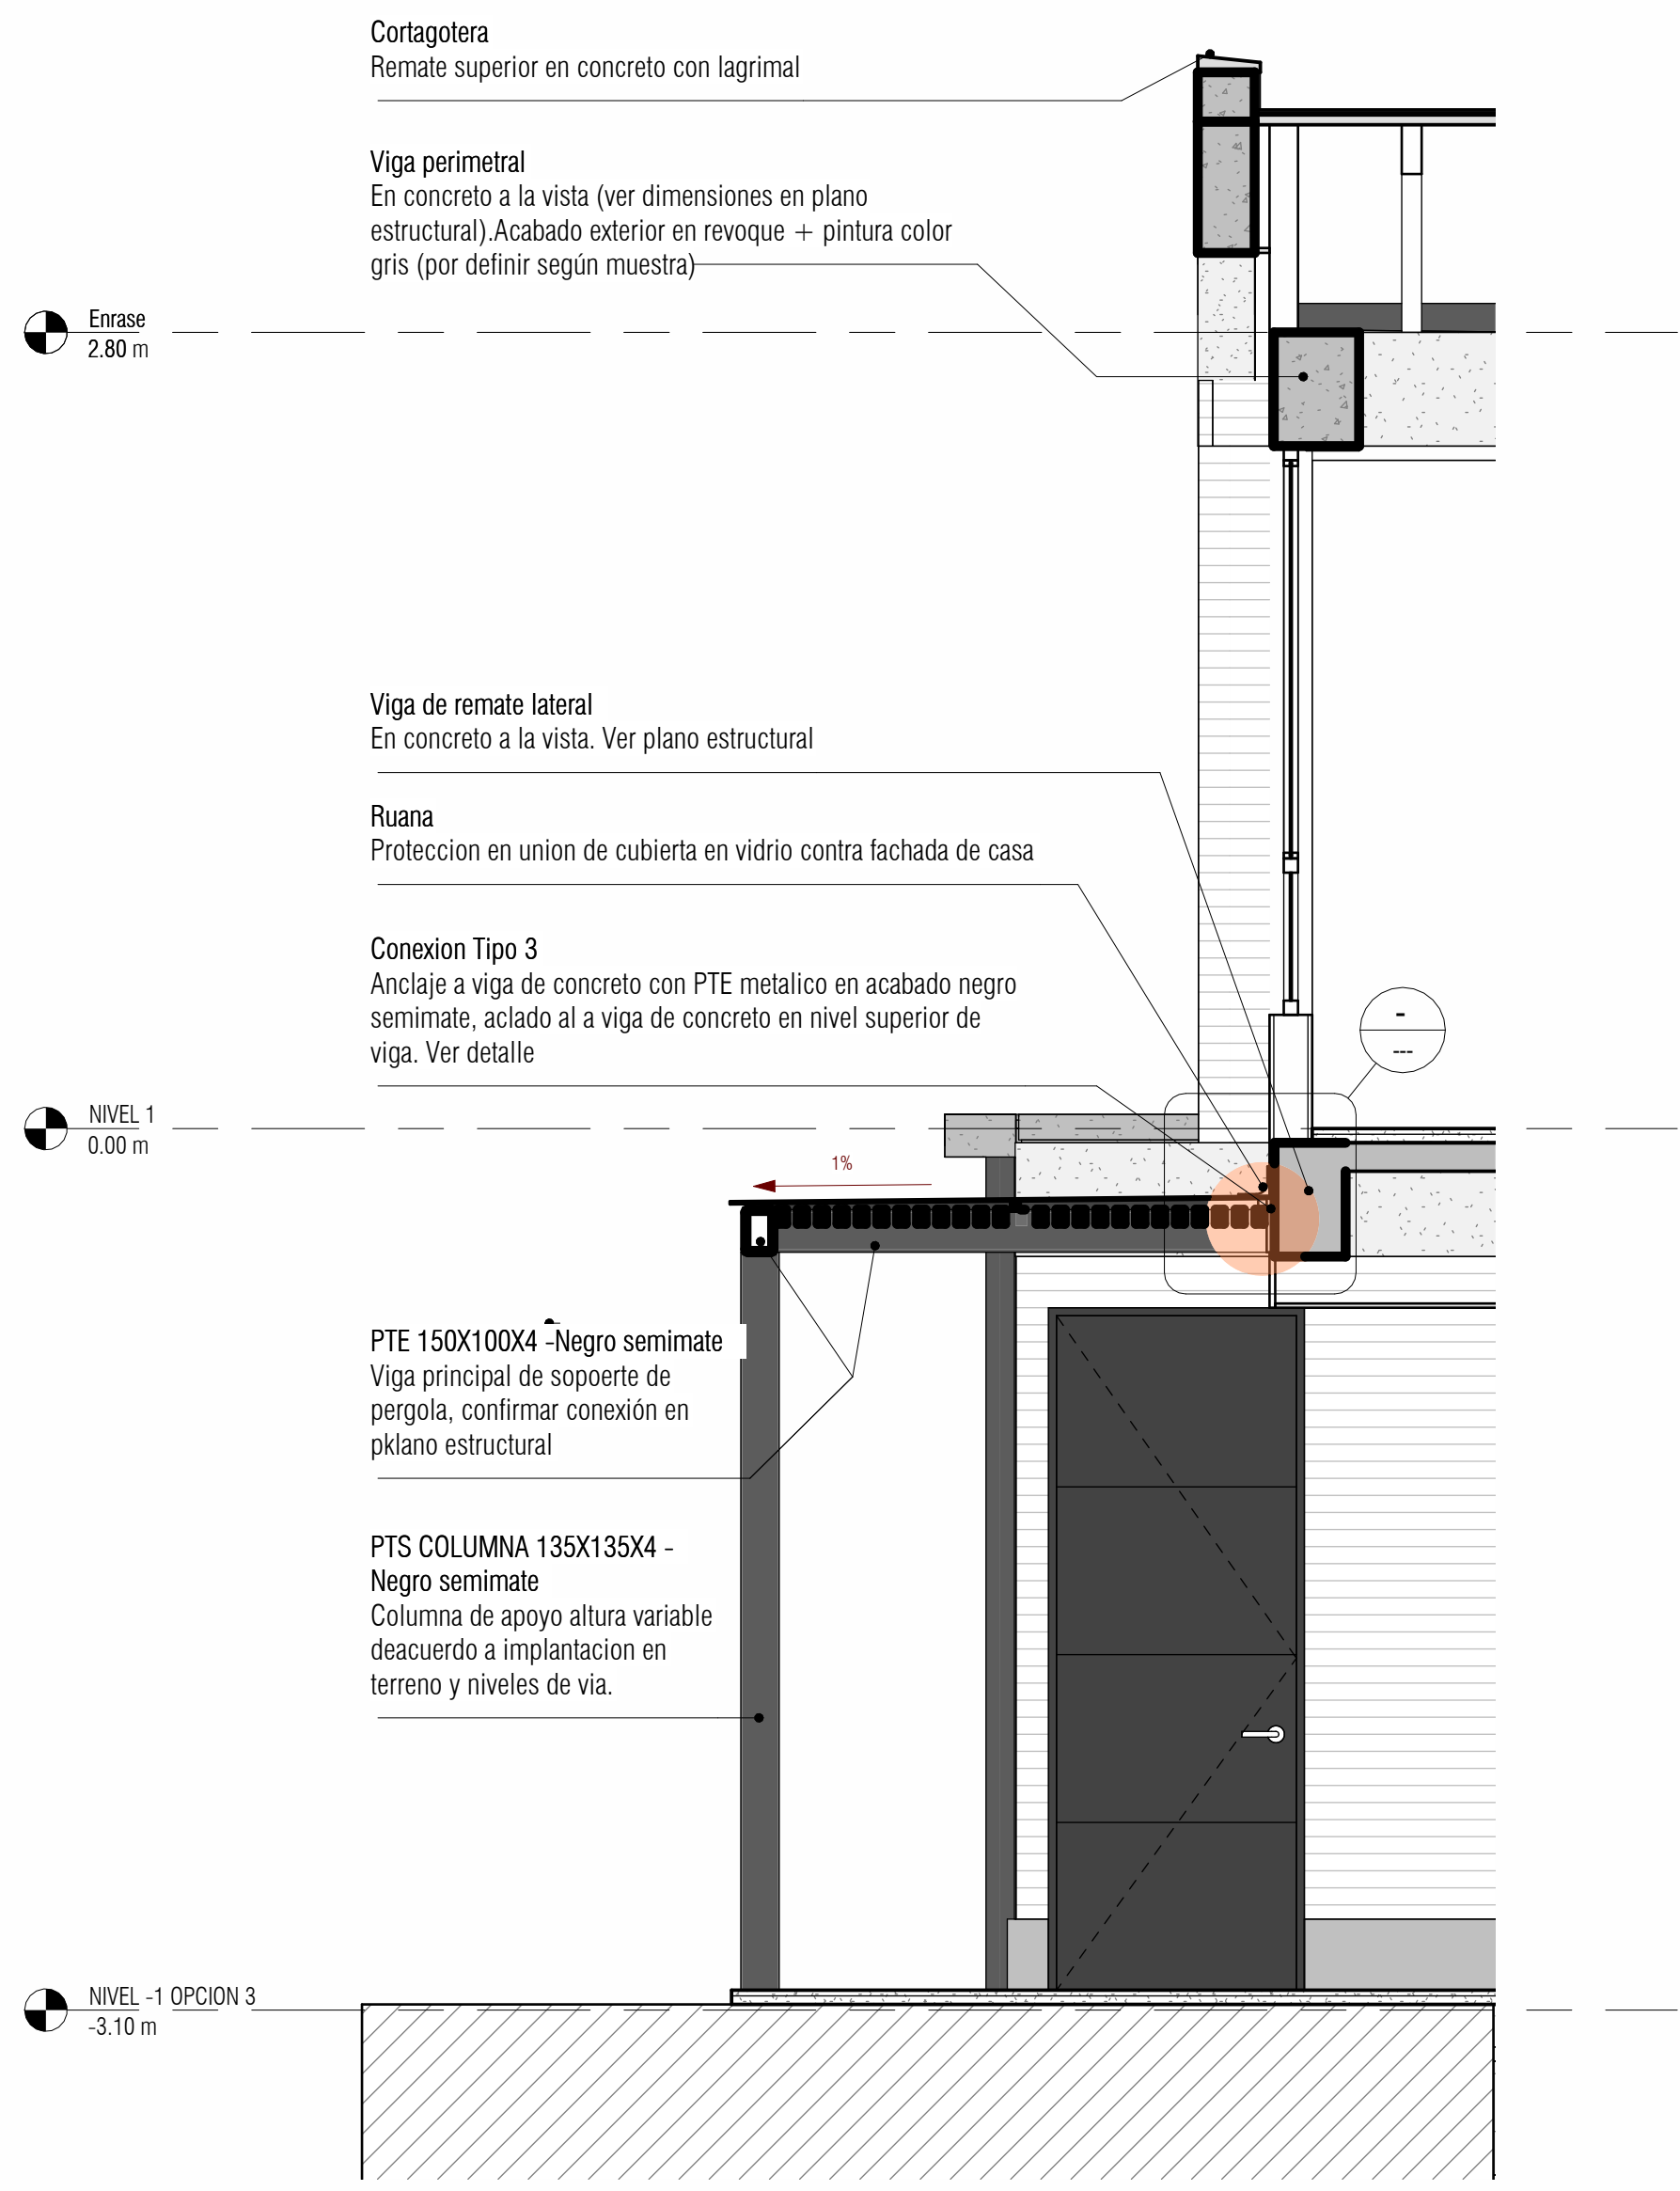

5 SECCIÓN TRANSVERSAL PERG. DECK
1:25

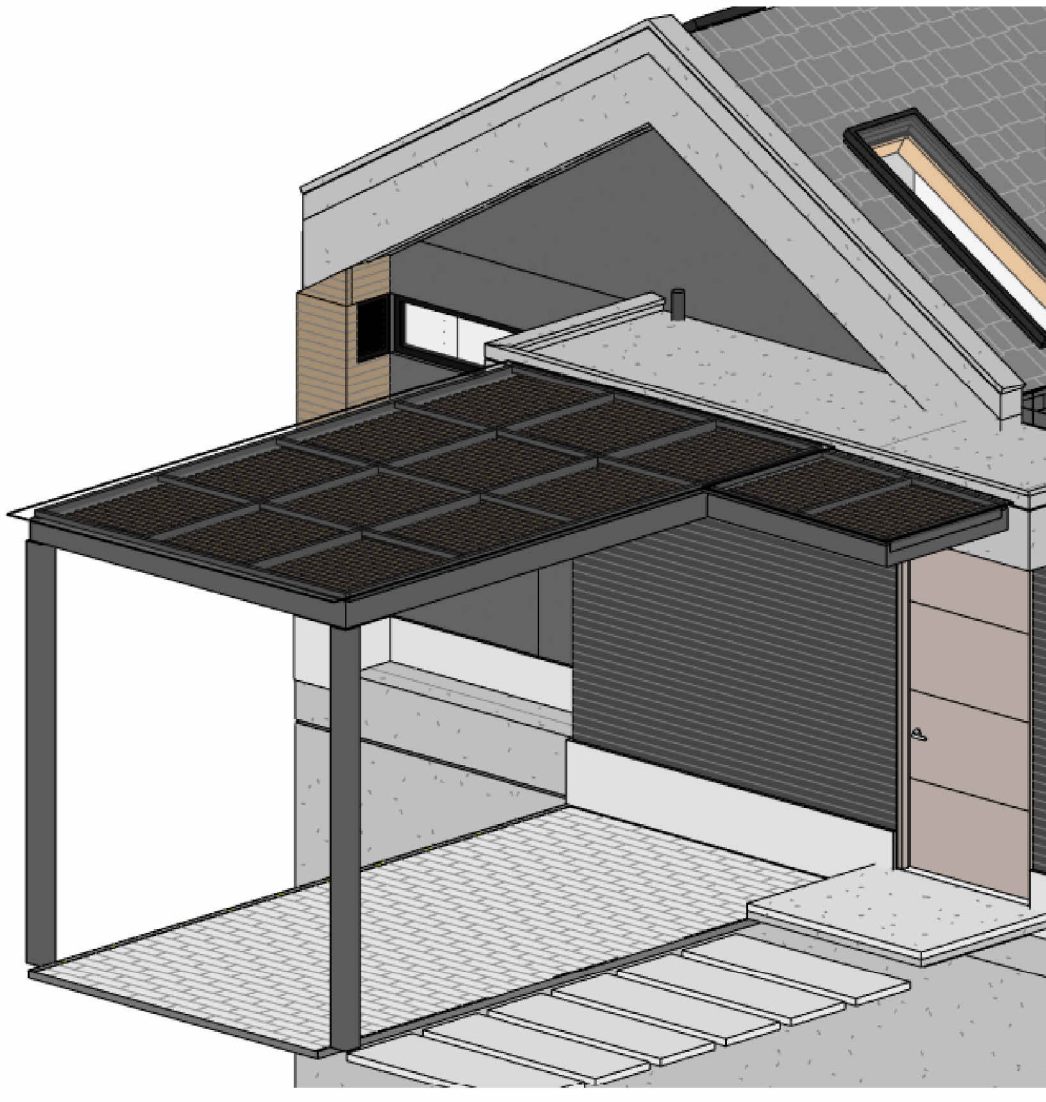


Imagen de referencia Pergola parqueadero + ingreso peatonal

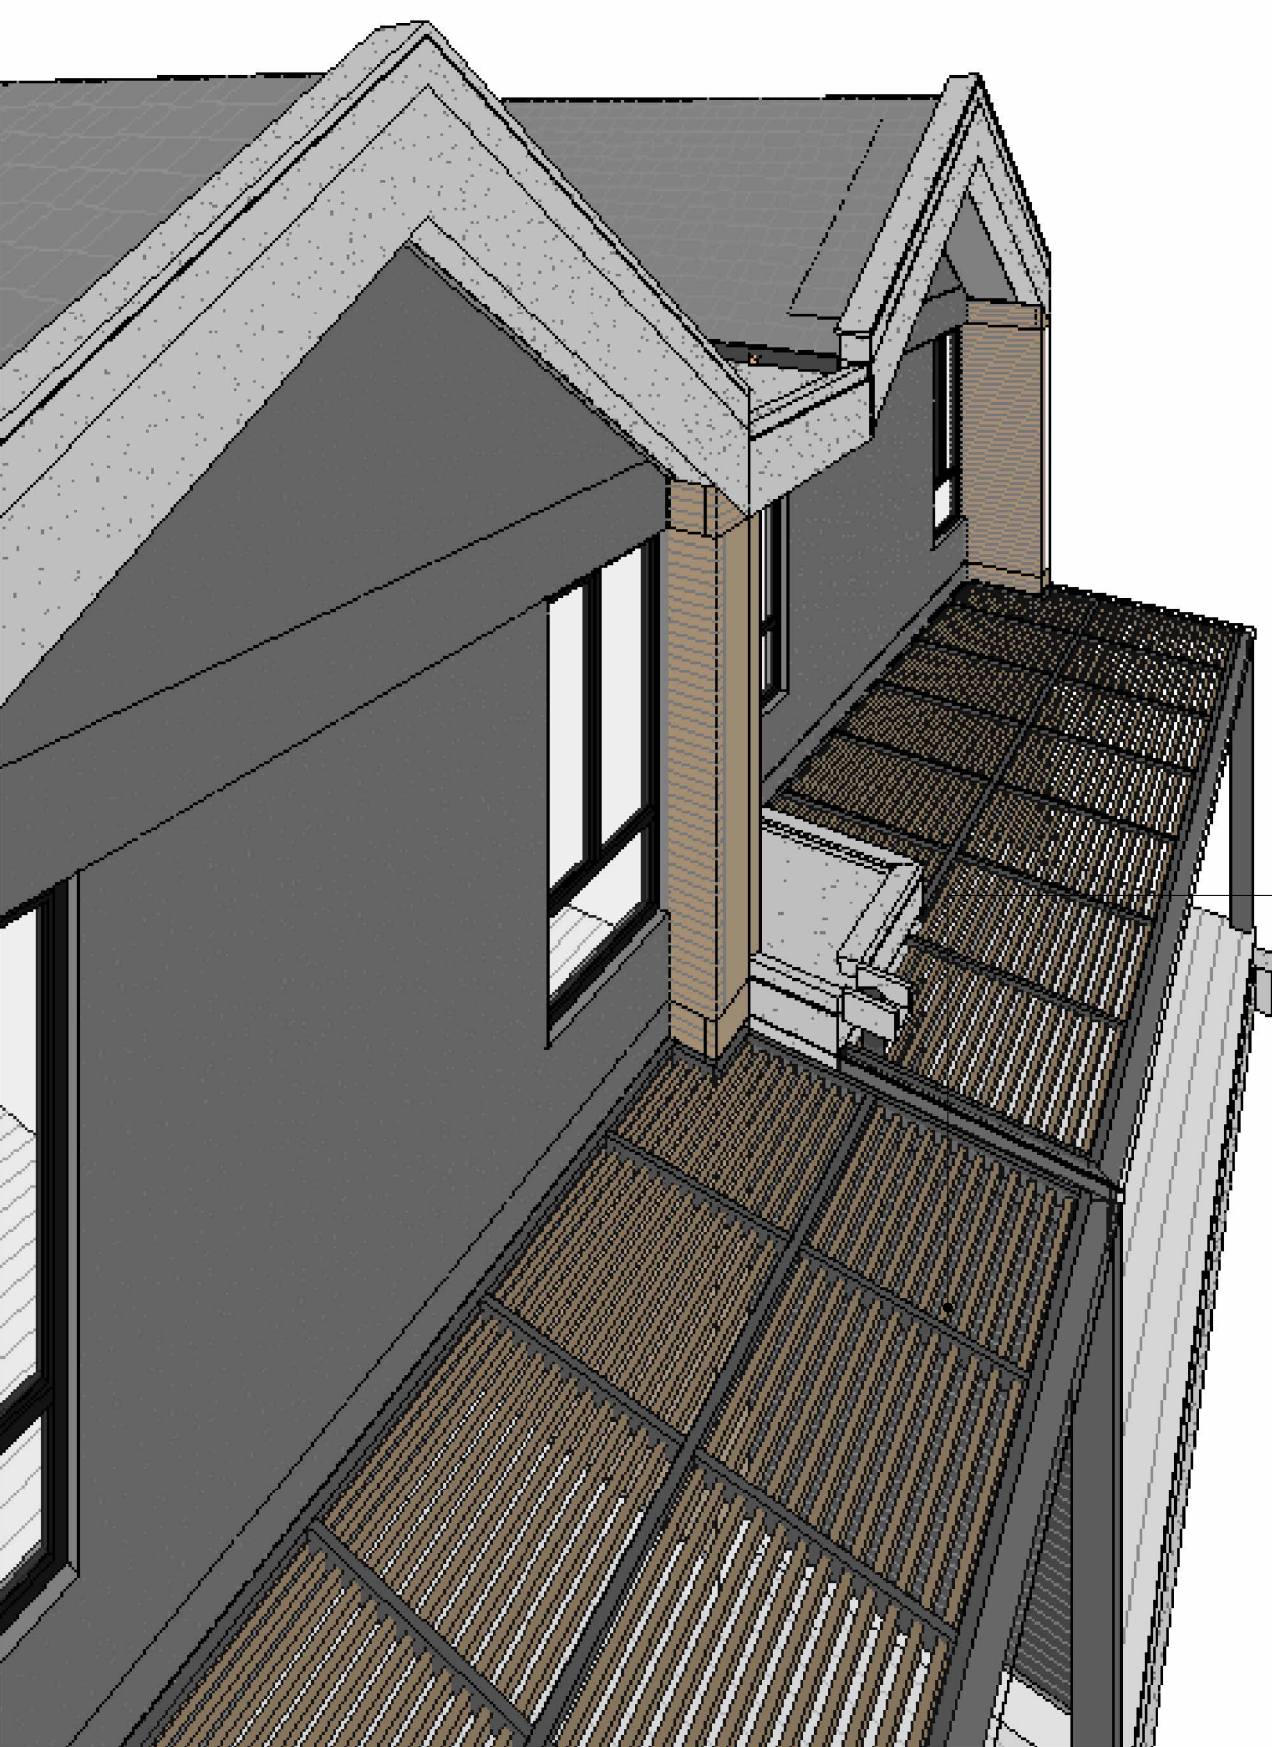


Imagen de referencia Pergola Deck